


IDD

Apartment Building

By
Giorgio Matheus Gatelli Magni
22141166


Sheet List		
Sheet Number	Sheet Name	Drawn By
A000	Cover Page	G. M.
A001	Sheet Schedule	G. M.
A100	Site Plan	G. M.
A101	Ground Floor	G. M.
A102	Ground Floor Realistic	G. M.
A103	First Floor	G. M.
A104	First Floor Realistic	G. M.
A105	Second Floor	G. M.
A106	Second Floor Realistic	G. M.
A107	Roof Level	G. M.
A200	West Elevation	G. M.
A201	North Elevation	G. M.
A202	East Elevation	G. M.
A300	Longitudinal Section	G. M.
A301	Lateral Section	G. M.
A400	Room Schedule - GR Floor	G. M.
A401	Room Schedule - 1st Floor	G. M.
A402	Room Schedule - 2nd Floor	G. M.
A403	Window Schedule	G. M.
A404	Door Schedule	G. M.
A405	Wall Schedule	G. M.
A500	Element Key - Windows	G. M.
A501	Element Key - Windows 2	G. M.
A502	Element Key - Windows 3	G. M.
A503	Element Key - Doors	G. M.
A600	3D Render 1	G. M.
A601	3D Render 2	G. M.
A602	3D Render 3	G. M.
A603	3D Render 4	G. M.

No.	Description	Date
CODE	SUITABILITY DESCRIPTION	
STATUS	PURPOSE OF ISSUE	
PROJECT		
IDD - Apartment Building		
TITLE		
Sheet Schedule		
CLIENT		
BCU Estates		
DRAWN BY G. M.	CHECKED BY G. M.	DATE Issue Date
SCALE (@A2)		PROJECT NUMBER INB202
DRAWING NUMBER A001		REV

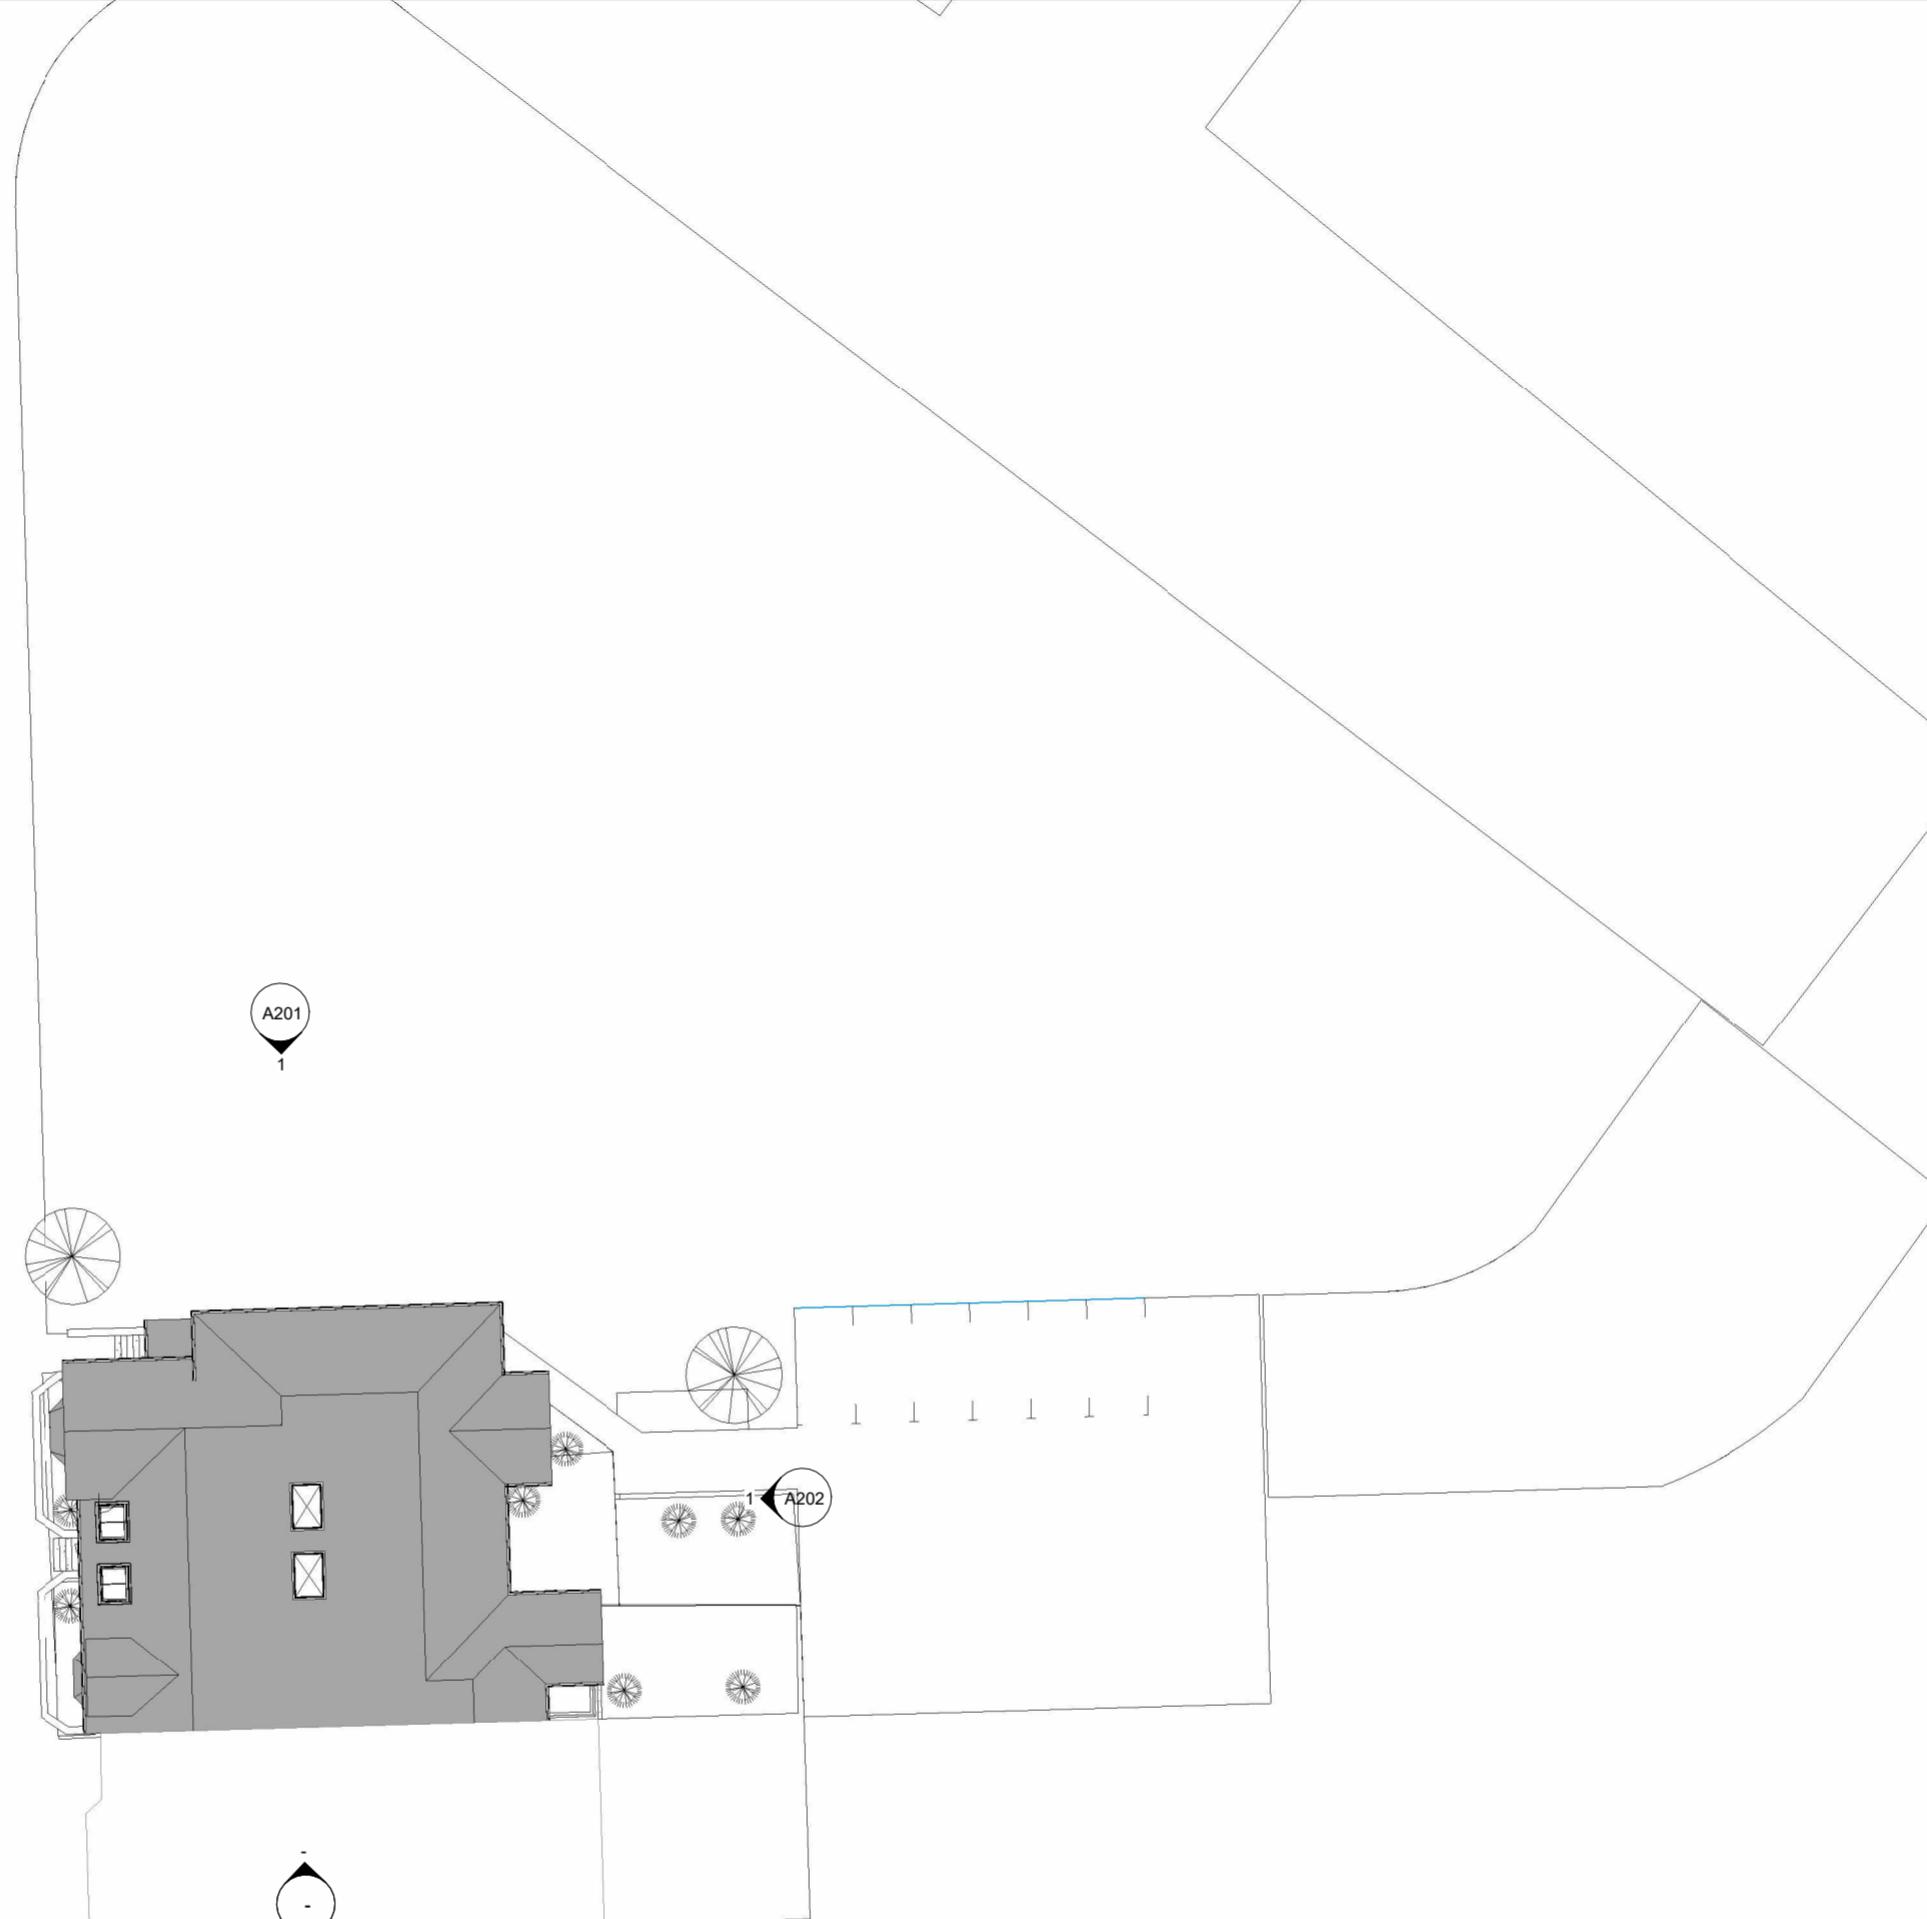

Site Plan

11/05/2023 13:55:56

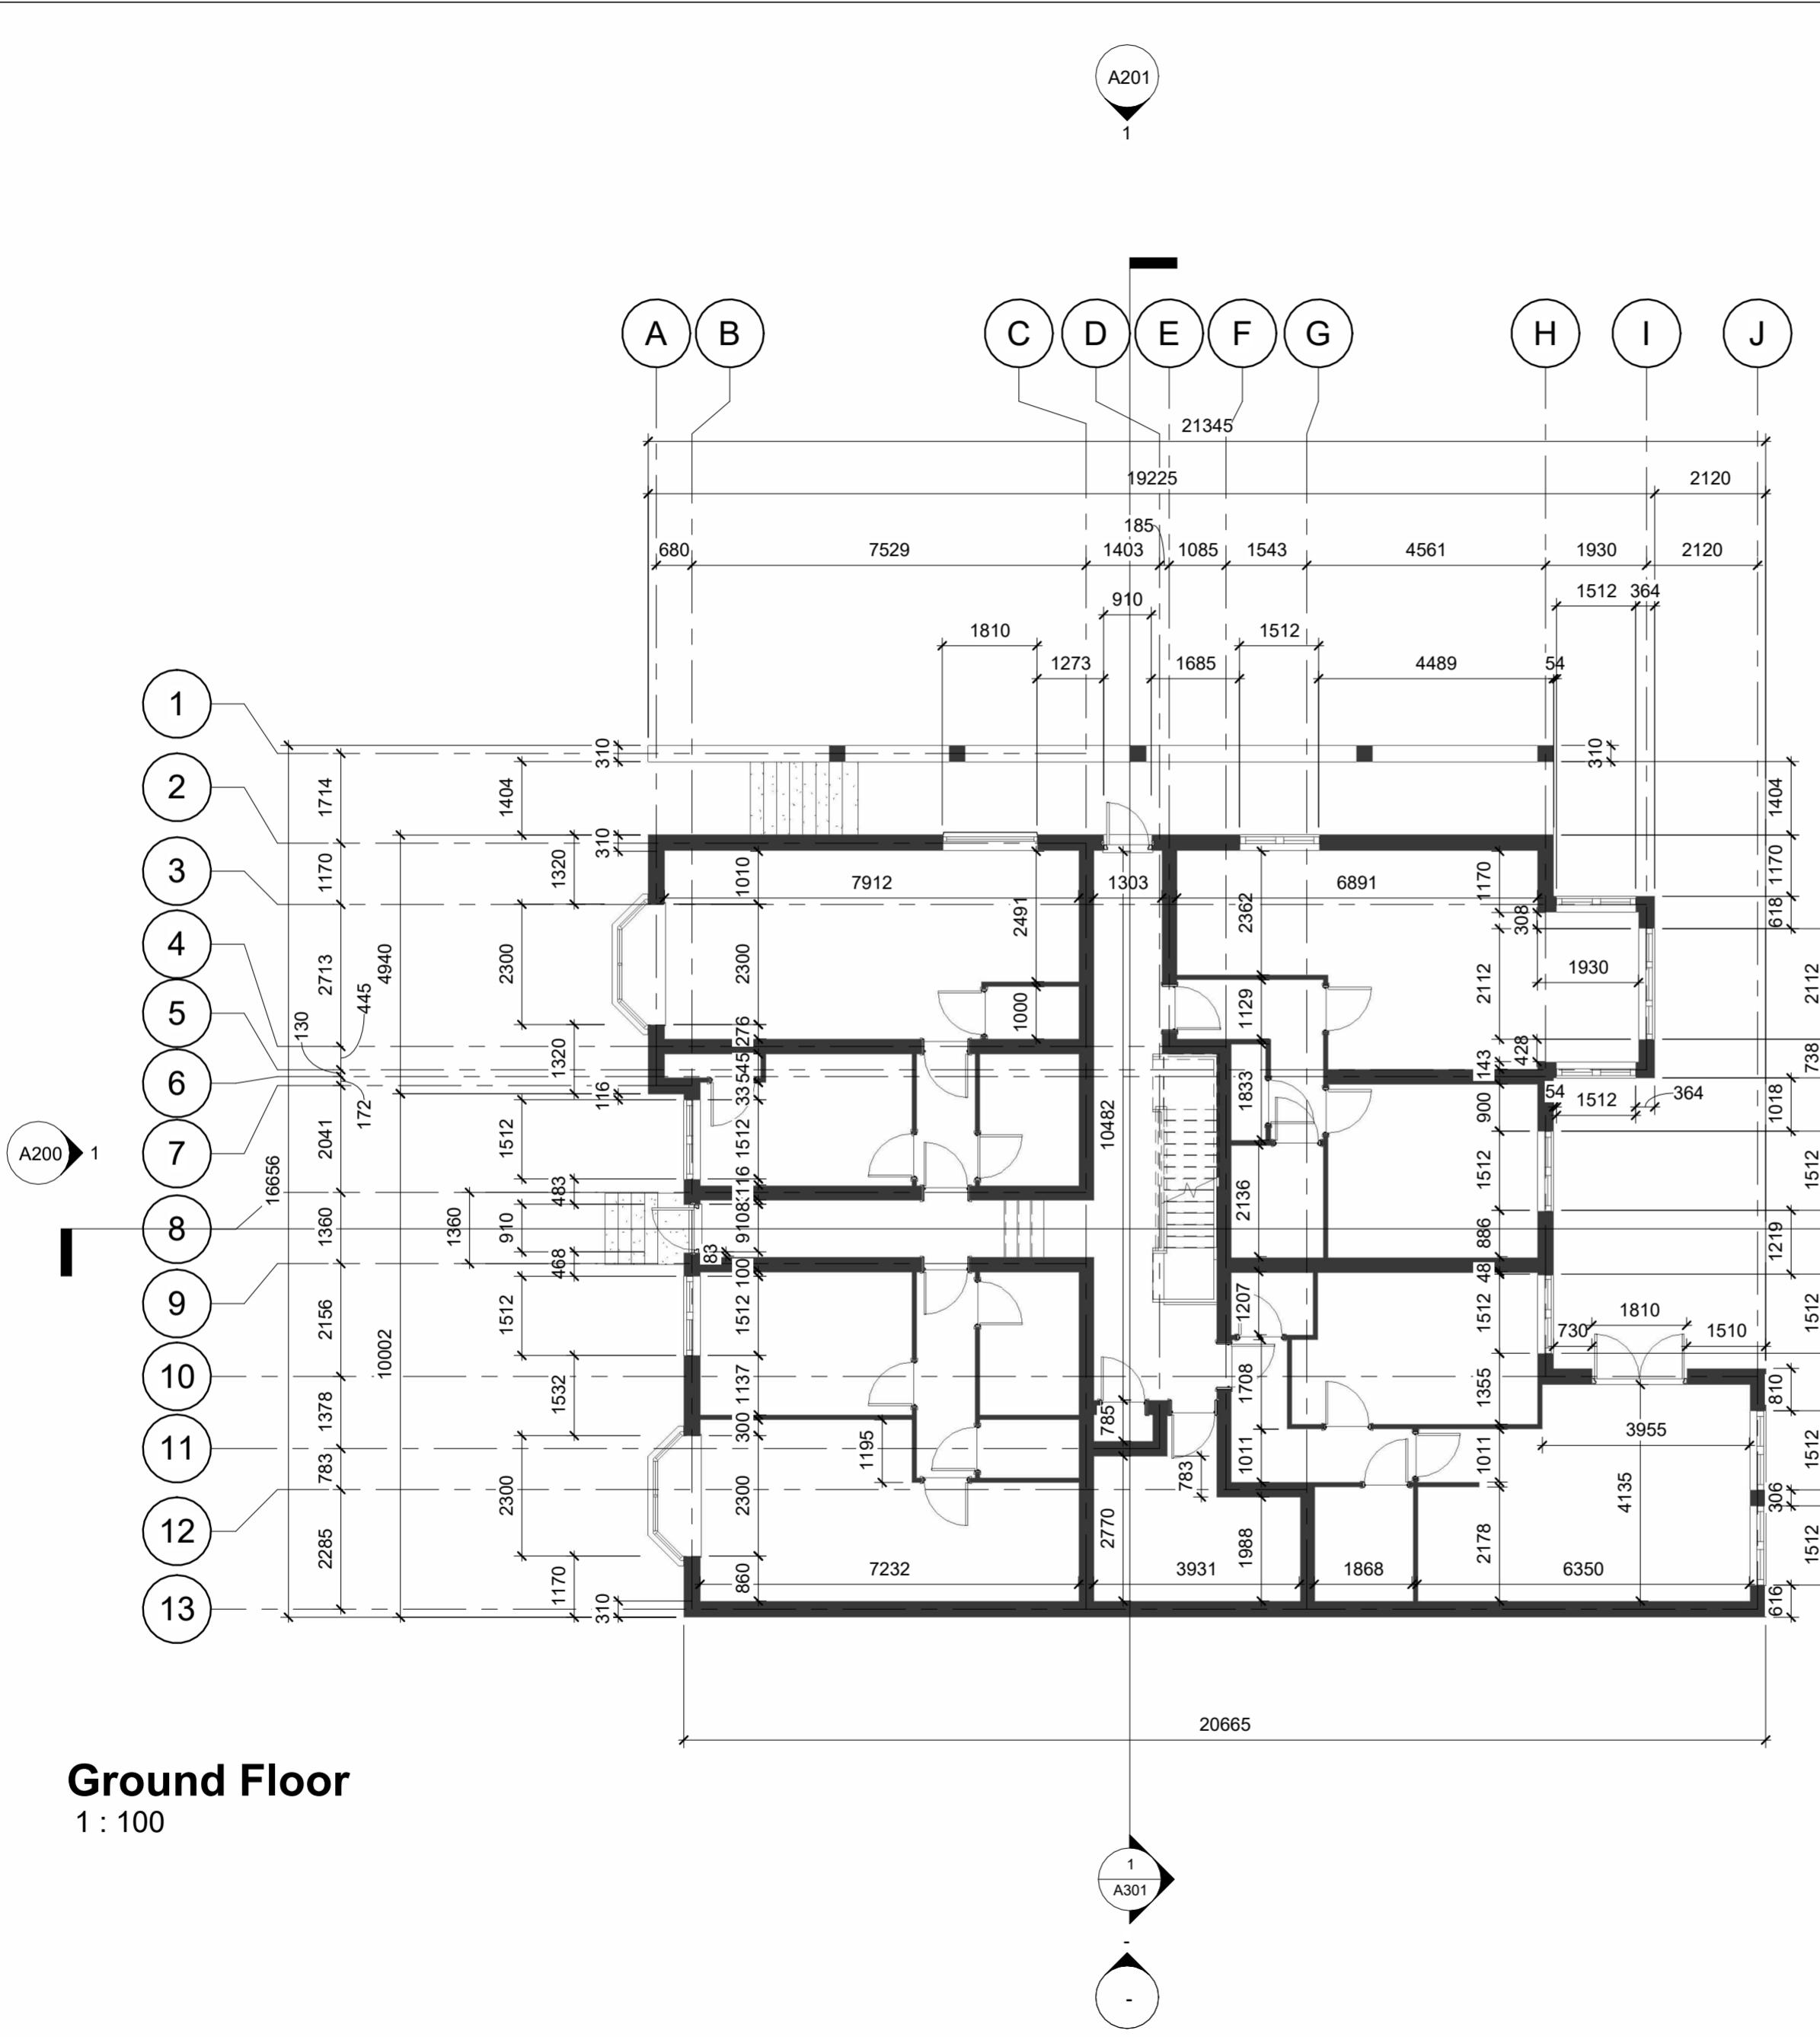


Ground Floor

1 : 100



Ground Floor Realistic

1 : 100

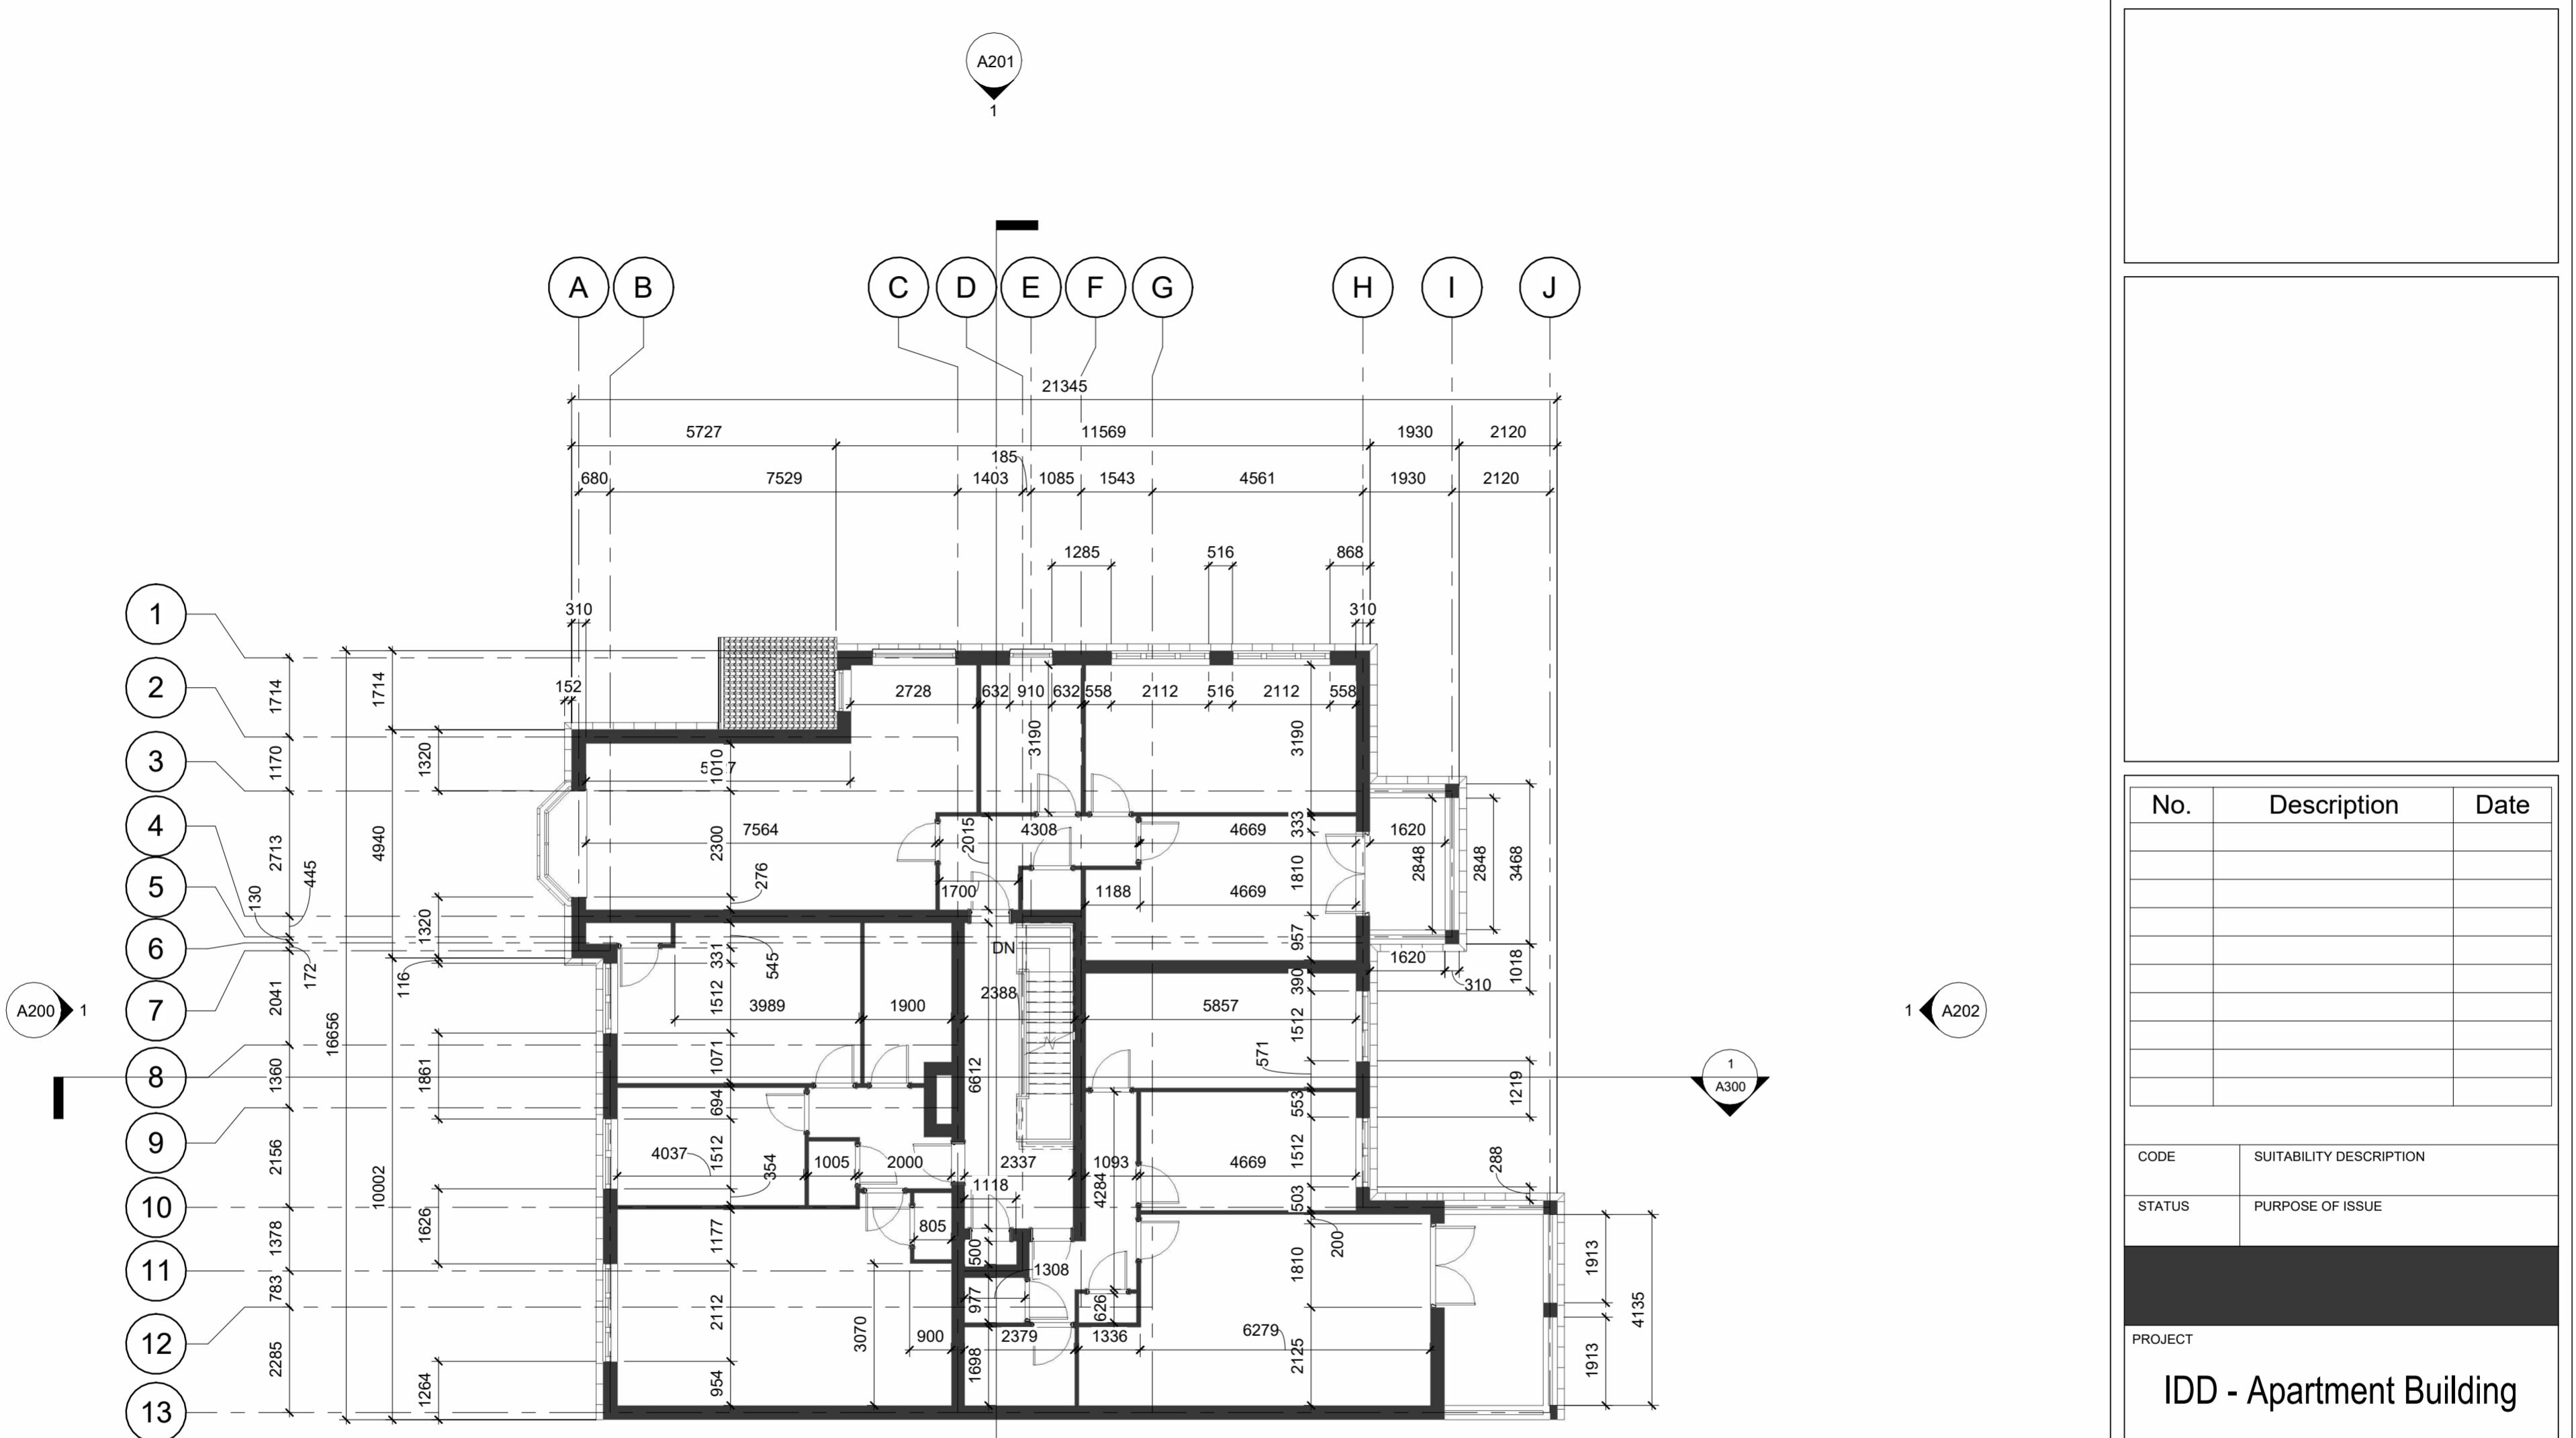


No.	Description	Date
PROJECT		
IDD - Apartment Building		
TITLE		
First Floor		
CLIENT		
BCU Estates		
DRAWN BY G. M.	CHECKED BY G. M.	DATE Issue Date
SCALE (@A2) 1 : 100		PROJECT NUMBER INB202
DRAWING NUMBER A103		REV



First Floor Realistic
1 : 100

No.	Description	Date		
CODE	SUITABILITY DESCRIPTION			
STATUS	PURPOSE OF ISSUE			
PROJECT				
IDD - Apartment Building				
TITLE				
First Floor Realistic				
CLIENT				
BCU Estates				
DRAWN BY G. M.	CHECKED BY G. M.	DATE Issue Date		
SCALE (@A2) 1 : 100	PROJECT NUMBER INB202			
DRAWING NUMBER A104	REV			

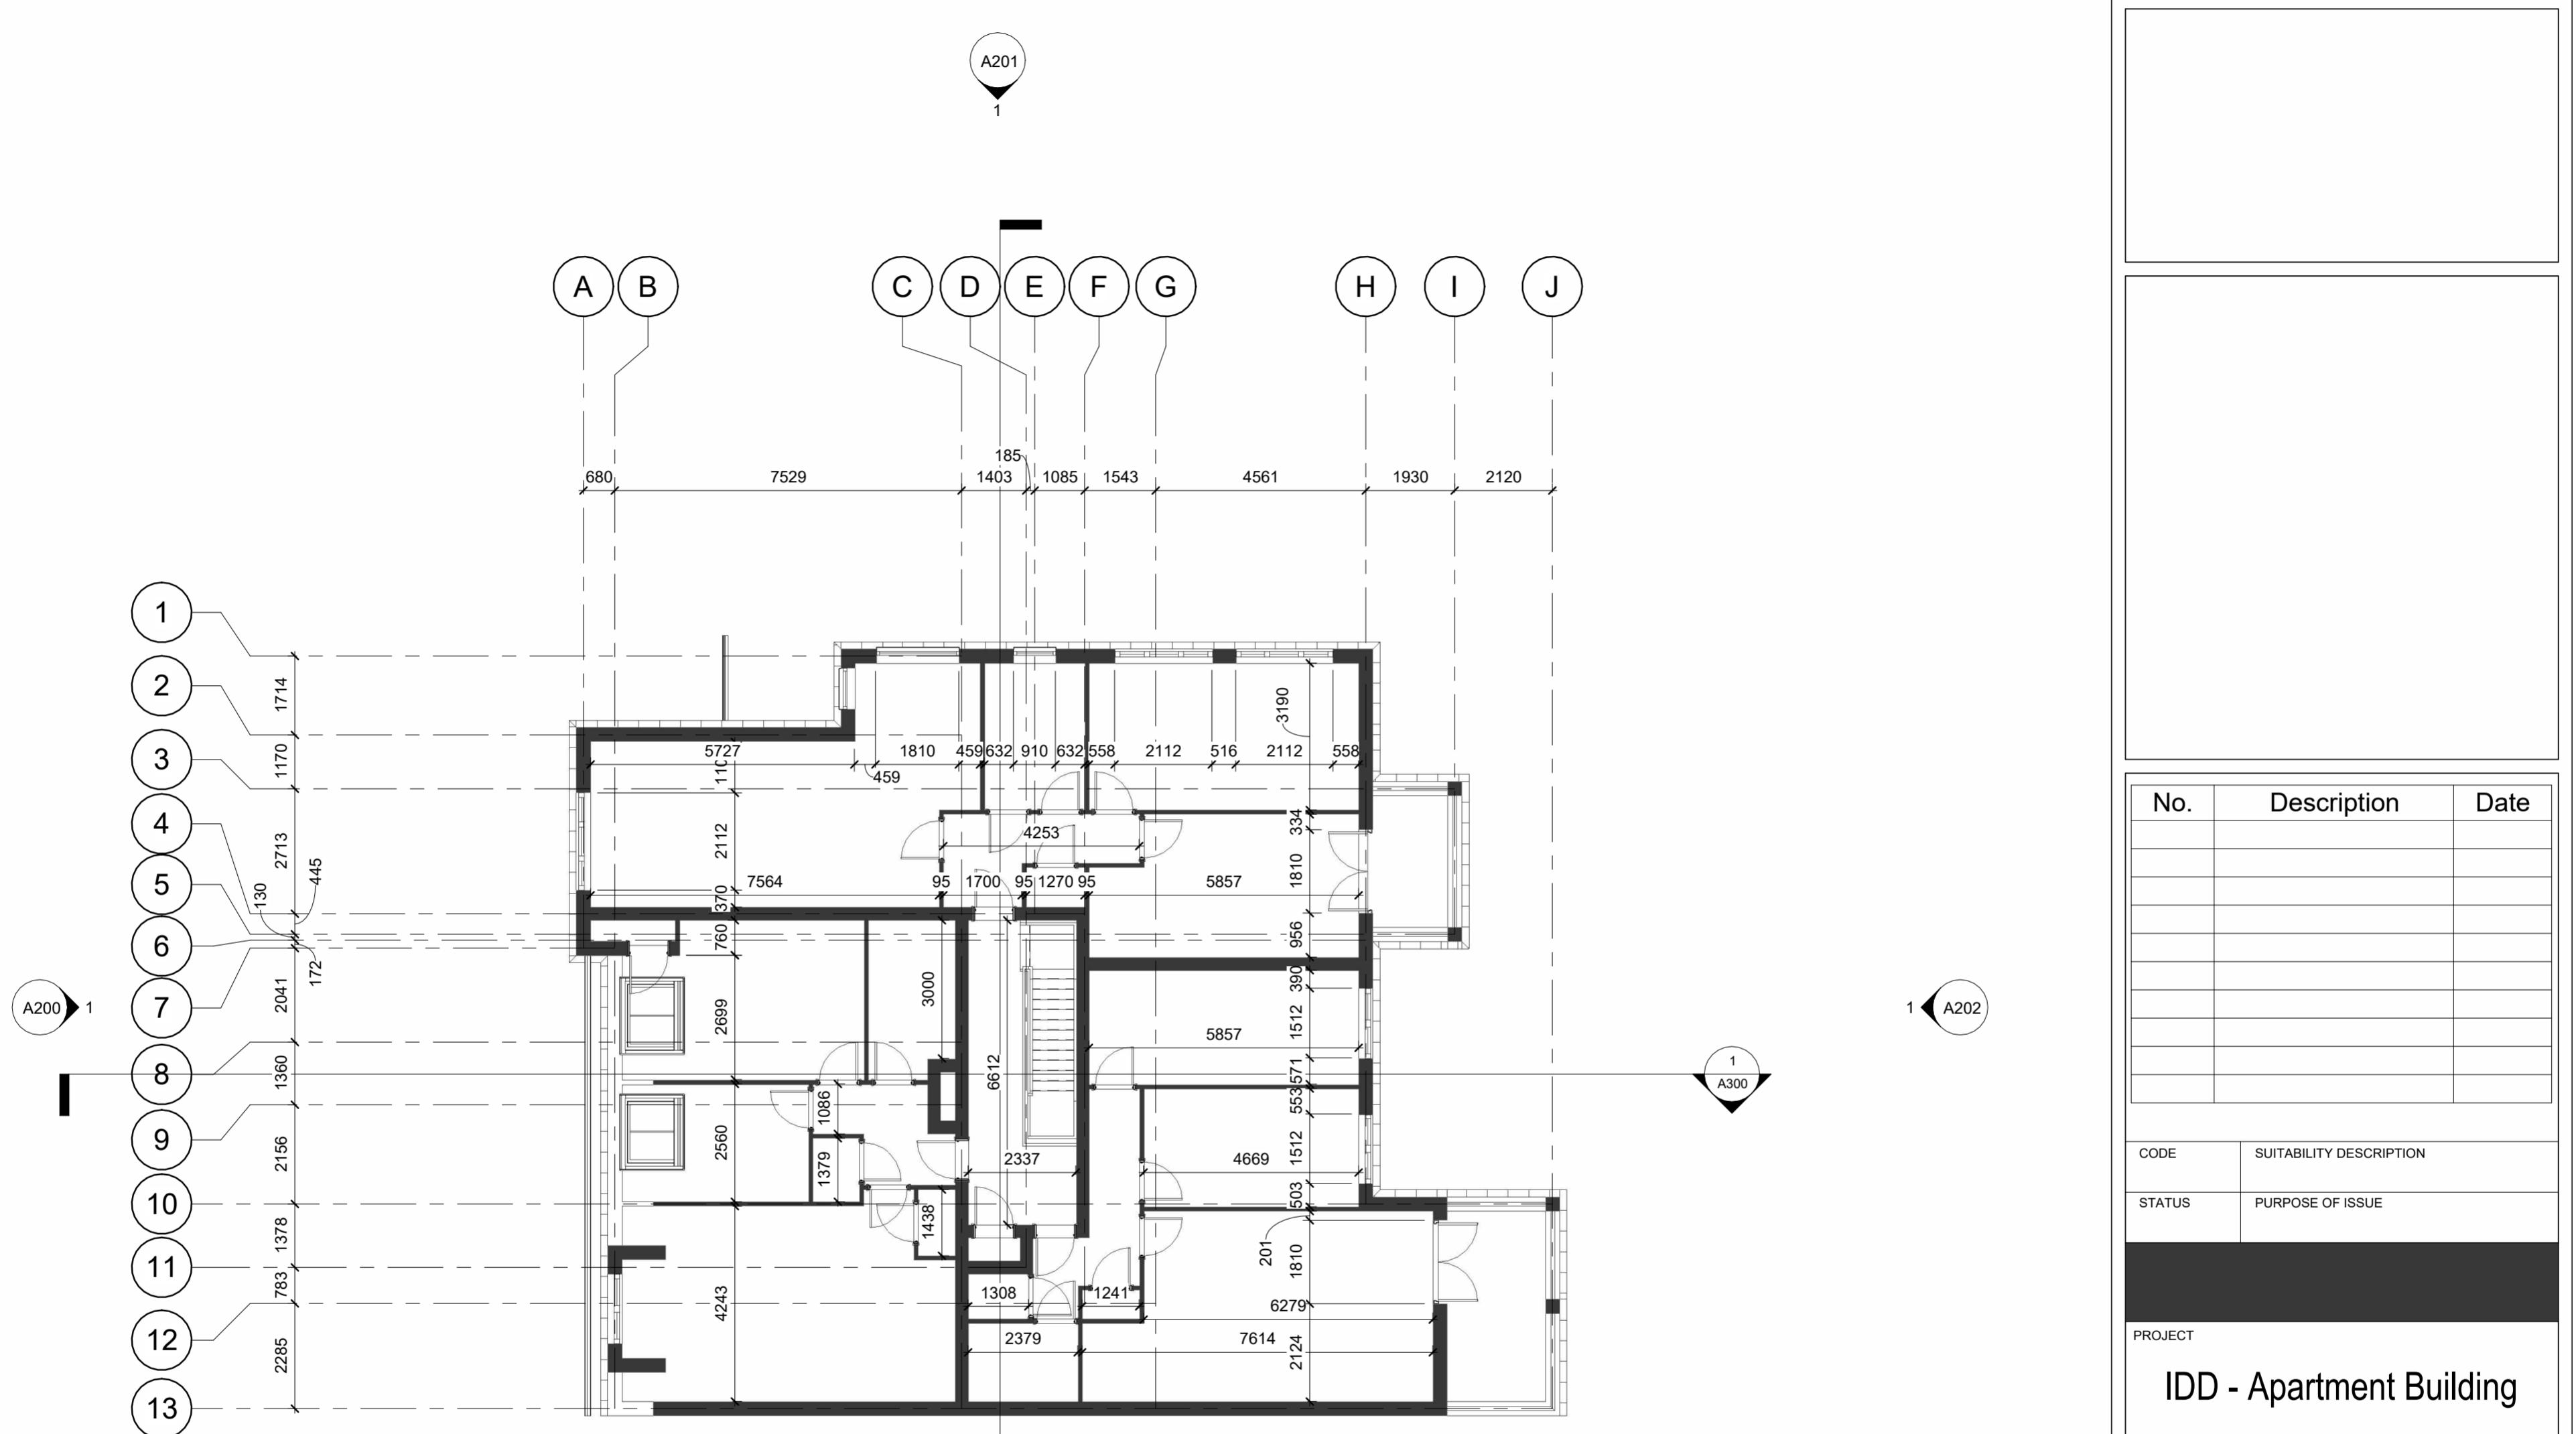

No.	Description	Date
PROJECT		
IDD - Apartment Building		
TITLE		
Second Floor		
CLIENT		
BCU Estates		
DRAWN BY G. M.	CHECKED BY G. M.	DATE Issue Date
SCALE (@A2) 1 : 100	PROJECT NUMBER INB202	REV
DRAWING NUMBER A105		




Second Floor Realistic

11/05/2023 13:56:14

Roof Level

1 : 100

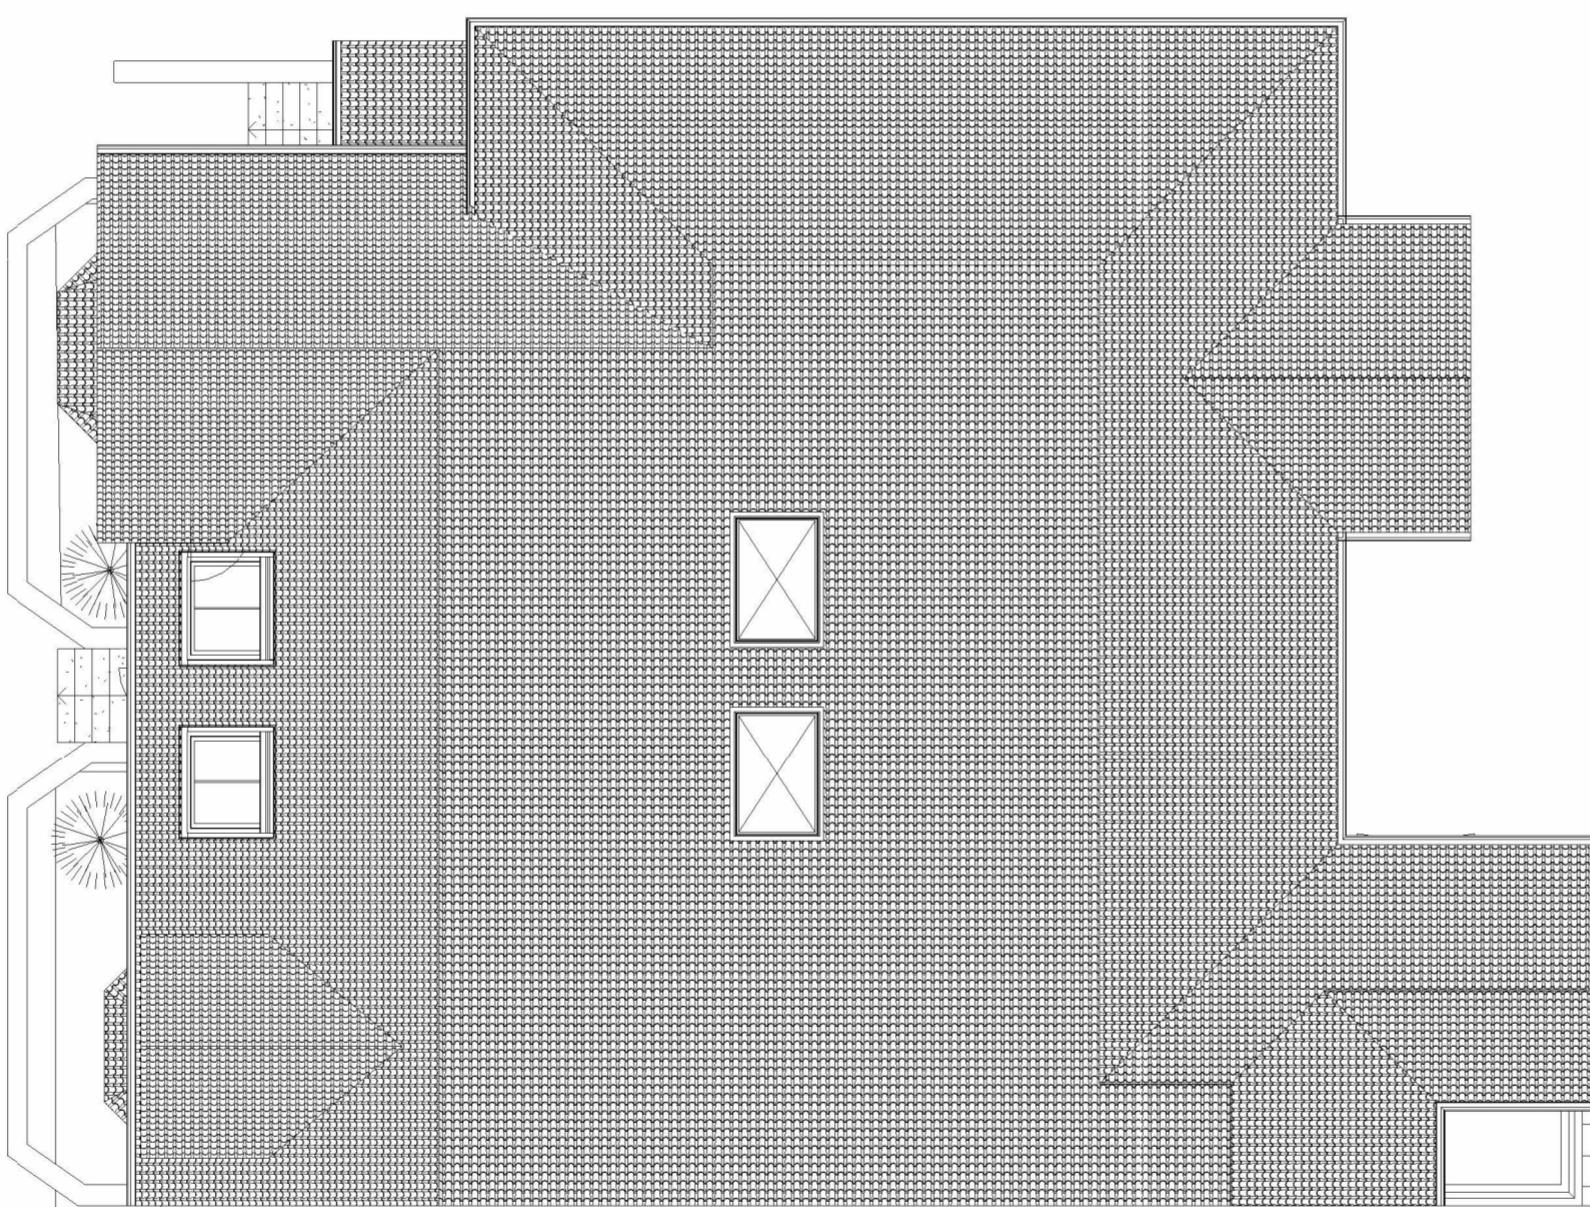

-

1

A200 1

1 A20

IDD - Apartment Building

Roof Level

BCU Estates

DRAWN BY G. M.	CHECKED BY G. M.	DATE Issue Date
SCALE (@A2) 1 : 100		PROJECT NUMBER INB202
DRAWING NUMBER A107		REV



WEST ELEVATION

1 : 75

No.	Description	Date
CODE	SUITABILITY DESCRIPTION	
STATUS	PURPOSE OF ISSUE	
PROJECT		
IDD - Apartment Building		
TITLE		
West Elevation		
CLIENT		
BCU Estates		
DRAWN BY G. M.	CHECKED BY G. M.	DATE Issue Date
SCALE (@A2) 1:75	PROJECT NUMBER INB202	
DRAWING NUMBER A200	REV	




11/05/2023 13:56:21

EAST ELEVATION


1 : 75



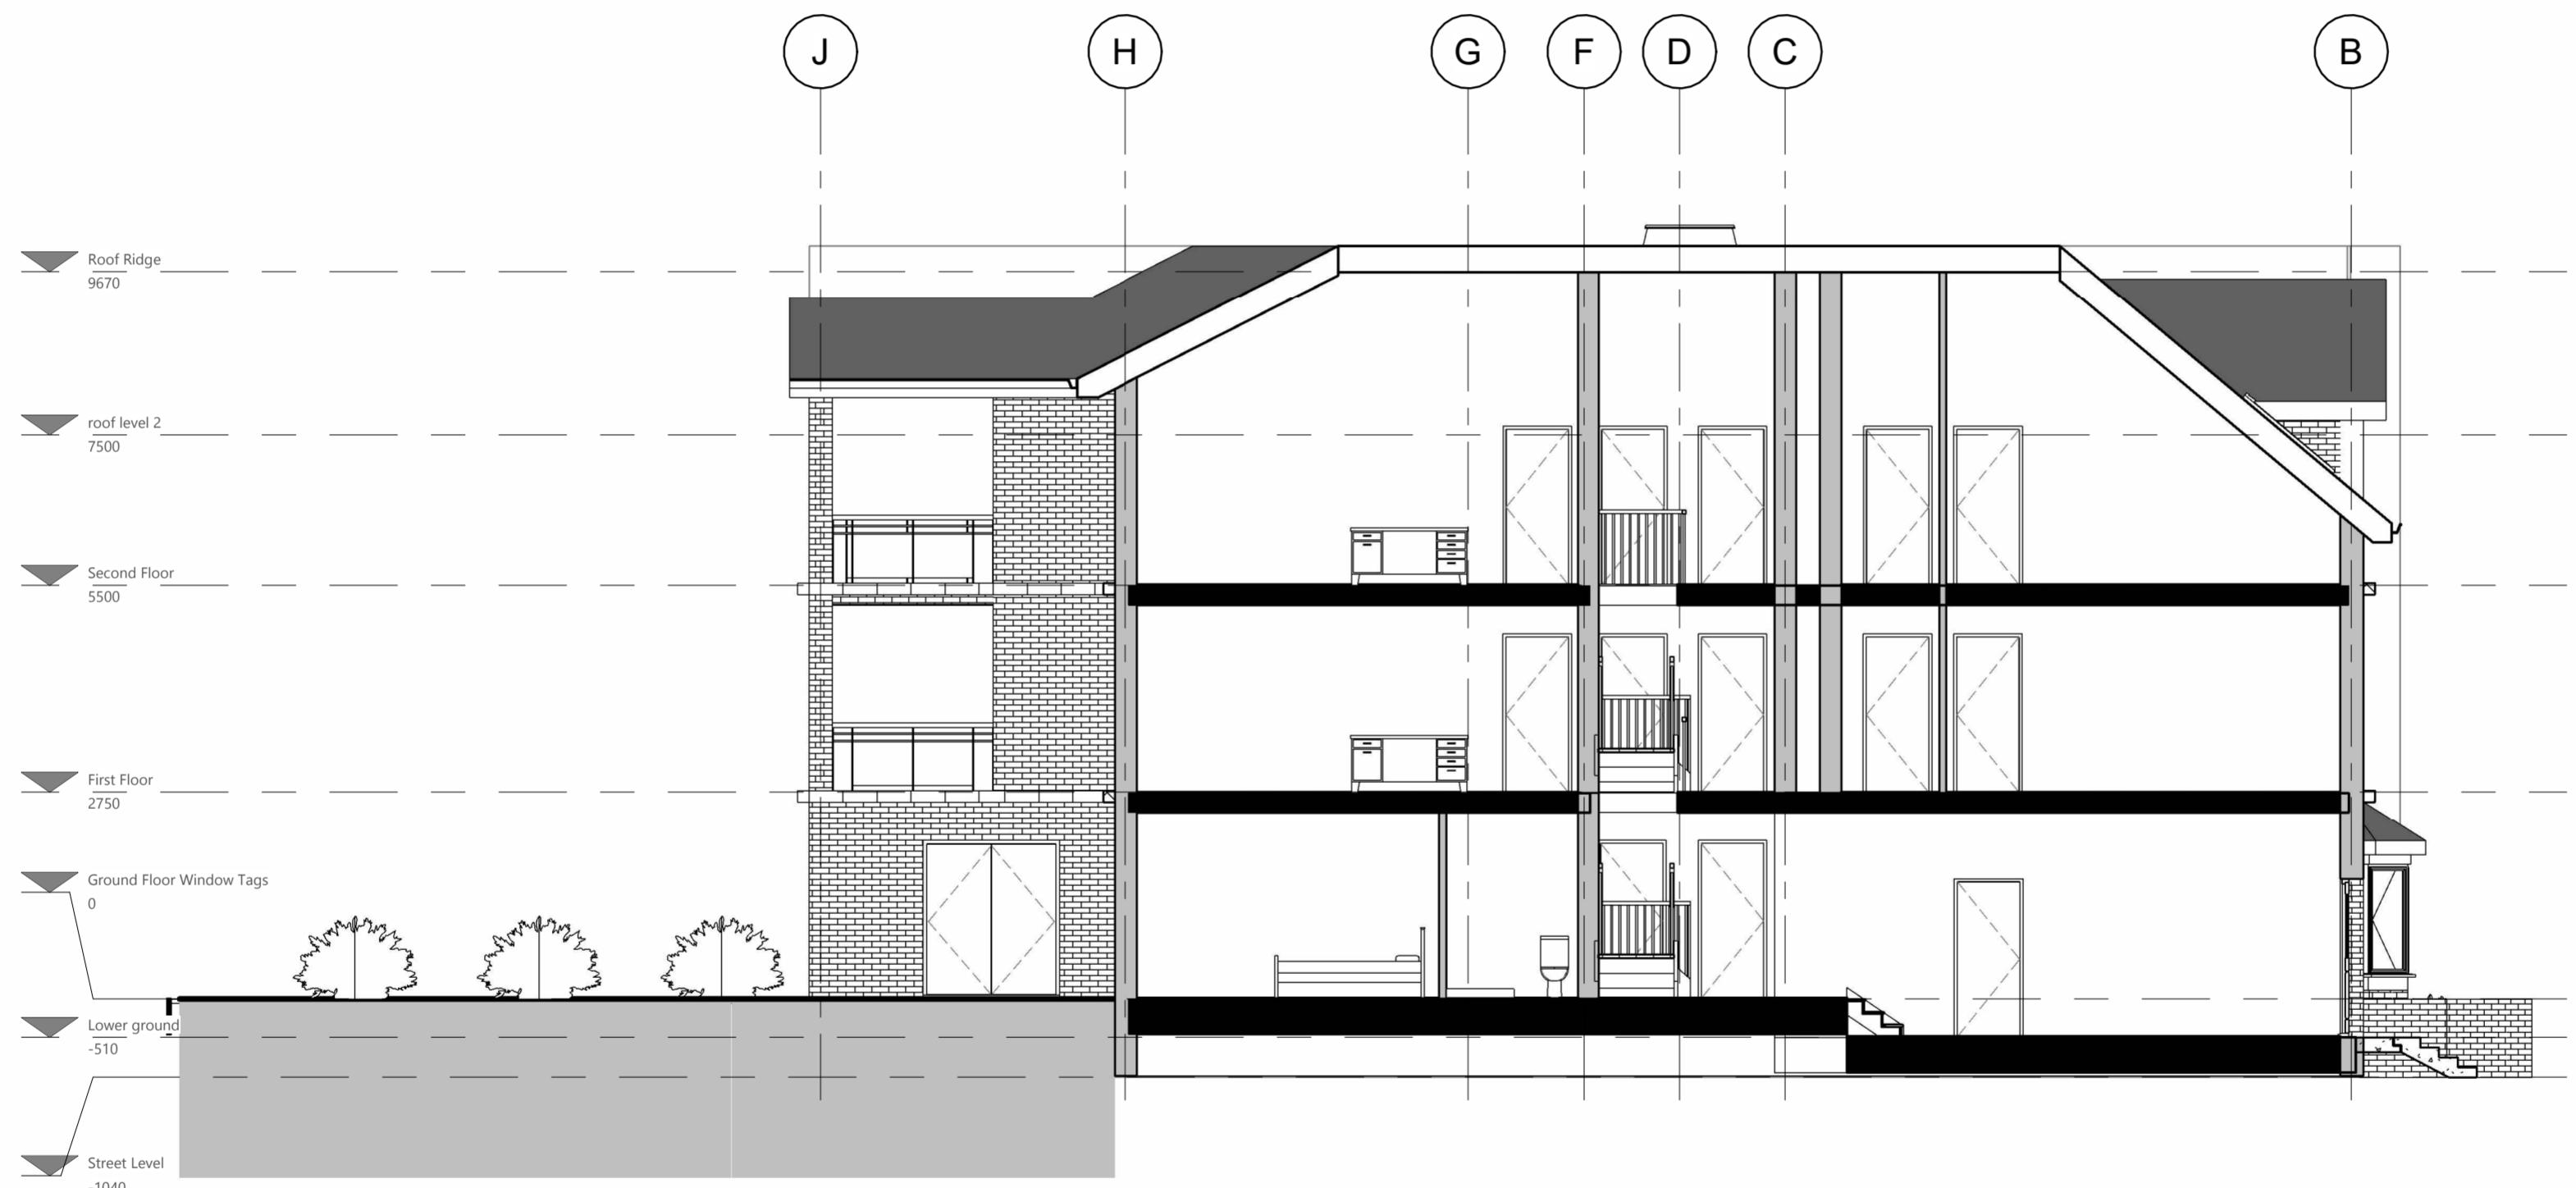

Longitudinal
1 : 75

No.	Description	Date		
CODE	SUITABILITY DESCRIPTION			
STATUS	PURPOSE OF ISSUE			
PROJECT				
IDD - Apartment Building				
TITLE				
Longitudinal Section				
CLIENT				
BCU Estates				
DRAWN BY G. M.	CHECKED BY G. M.	DATE Issue Date		
SCALE (@A2) 1:75	PROJECT NUMBER INB202			
DRAWING NUMBER A300		REV		

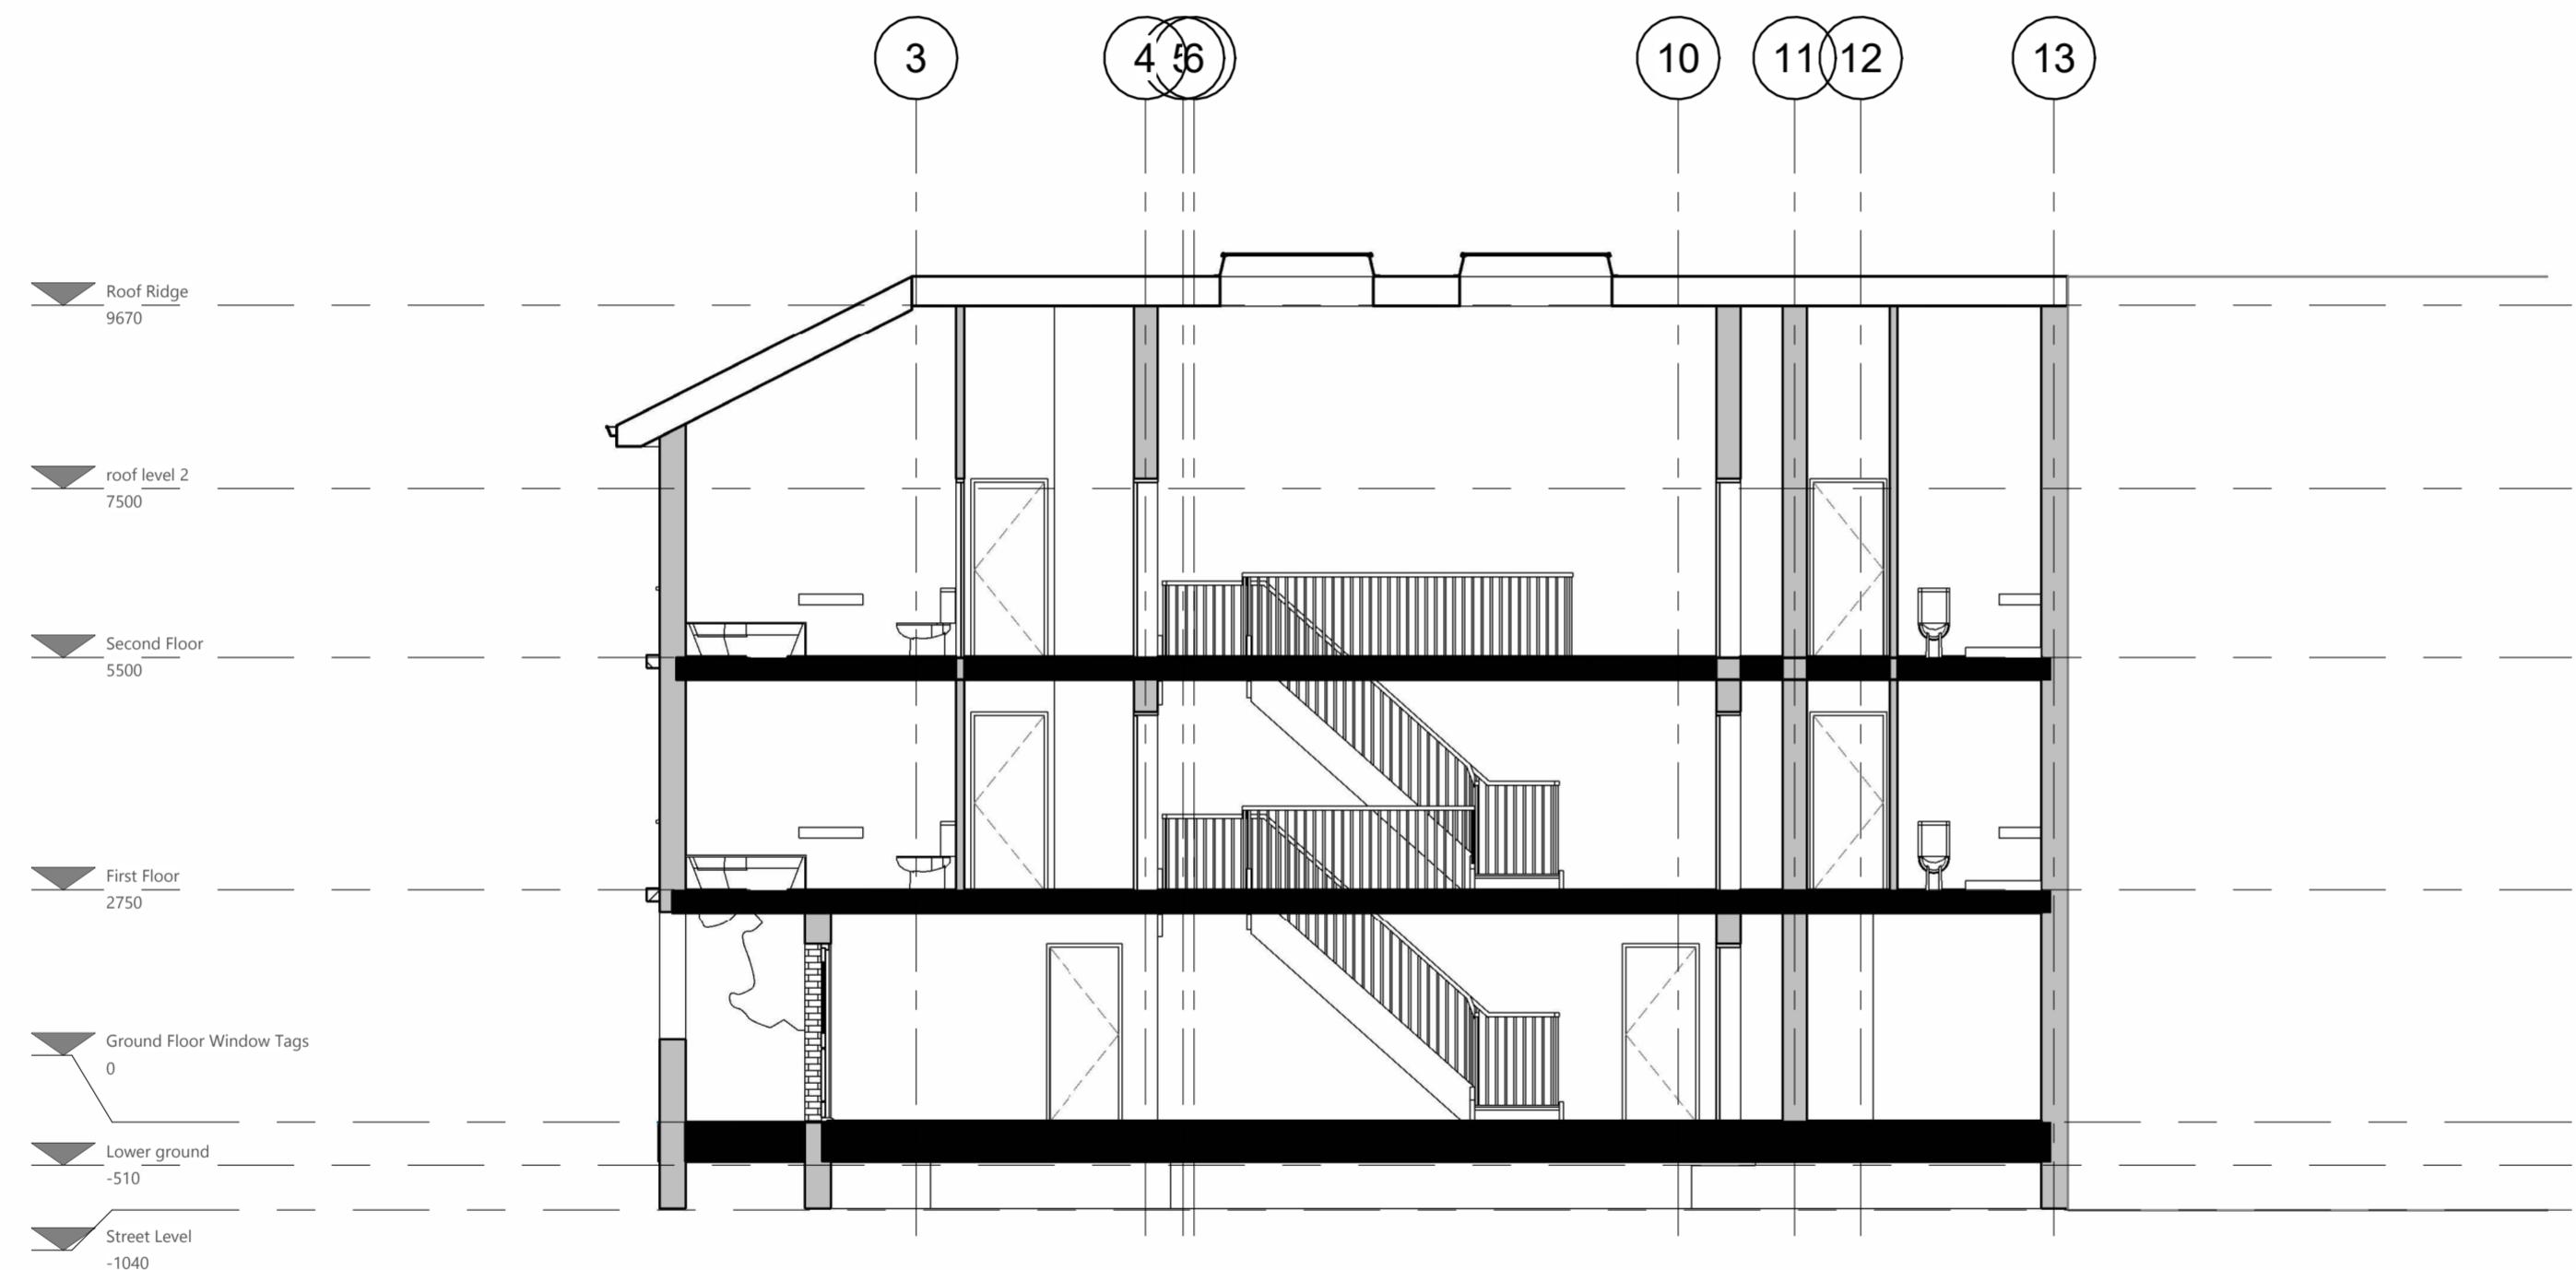

Lateral
1 : 75

No.	Description	Date
CODE	SUITABILITY DESCRIPTION	
STATUS	PURPOSE OF ISSUE	
PROJECT		
IDD - Apartment Building		
TITLE		
Lateral Section		
CLIENT		
BCU Estates		
DRAWN BY G. M.	CHECKED BY G. M.	DATE Issue Date
SCALE (@A2) 1:75	PROJECT NUMBER INB202	
DRAWING NUMBER A301	REV	



1 **Ground Floor Room Tags (Furnished)**

1 : 100

Room Schedule		
Name	Level	Area

Ground Floor Window Tags

Bathroom	Ground Floor Window Tags	5 m ²
Bathroom	Ground Floor Window Tags	5 m ²
Bathroom	Ground Floor Window Tags	4 m ²
Bathroom	Ground Floor Window Tags	4 m ²
Bedroom	Ground Floor Window Tags	11 m ²
Bedroom	Ground Floor Window Tags	13 m ²
Bedroom	Ground Floor Window Tags	13 m ²
Bedroom	Ground Floor Window Tags	9 m ²
Communal Hallway	Ground Floor Window Tags	29 m ²
Gym	Ground Floor Window Tags	10 m ²
Hallway	Ground Floor Window Tags	4 m ²
Hallway	Ground Floor Window Tags	5 m ²
Hallway	Ground Floor Window Tags	5 m ²
Hallway	Ground Floor Window Tags	3 m ²
Living Room/Kitchen	Ground Floor Window Tags	26 m ²
Living Room/Kitchen	Ground Floor Window Tags	29 m ²
Living Room/Kitchen	Ground Floor Window Tags	24 m ²
Living room/Kitchen	Ground Floor Window Tags	21 m ²
Storage	Ground Floor Window Tags	2 m ²
Storage	Ground Floor Window Tags	2 m ²
Storage	Ground Floor Window Tags	1 m ²
Storage	Ground Floor Window Tags	2 m ²
Storage	Ground Floor Window Tags	1 m ²
Storage	Ground Floor Window Tags	1 m ²

Ground Floor Window Tags: 24

No.	Description	Date
-----	-------------	------

CODE	SUITABILITY DESCRIPTION
STATUS	PURPOSE OF ISSUE

PROJECT	
IDD - Apartment Building	

TITLE	
Room Schedule - GR Floor	

CLIENT	
BCU Estates	

DRAWN BY G. M.	CHECKED BY G. M.	DATE Issue Date
-------------------	---------------------	--------------------

SCALE (@A2) 1 : 100	PROJECT NUMBER INB202
------------------------	--------------------------

DRAWING NUMBER A400	REV
------------------------	-----



First Floor Room Tags (Furnished)

1 : 100

Room Schedule		
Name	Level	Area

First Floor

First Floor: 25

A large, empty rectangular frame occupies most of the page, positioned to the right of the vertical margin line. It appears to be a placeholder for an image or diagram that has not been inserted.

No.	Description	Date
CODE	SUITABILITY DESCRIPTION	
STATUS	PURPOSE OF ISSUE	

PROJECT

IDD - Apartment Building

TITLE

Room Schedule - 1st Floor

CLIENT

BCU Estates

DRAWN BY G. M.	CHECKED BY G. M.	DATE Issue Date
SCALE (@A2) 1 : 100	PROJECT NUMBER INB202	
DRAWING NUMBER A401		REV




Second Floor Room Tags (Furnished)

1 : 100

Room Schedule		
Name	Level	Area
Second Floor		
Balcony	Second Floor	9 m ²
Balcony	Second Floor	5 m ²
Bathroom	Second Floor	6 m ²
Bathroom	Second Floor	4 m ²
Bedroom	Second Floor	10 m ²
Bedroom	Second Floor	17 m ²
Bedroom	Second Floor	19 m ²
Bedroom	Second Floor	14 m ²
Bedroom	Second Floor	12 m ²
Bedroom	Second Floor	17 m ²
Communal Hallway	Second Floor	15 m ²
Hallway	Second Floor	5 m ²
Hallway	Second Floor	6 m ²
Hallway	Second Floor	7 m ²
Living Room/Kitchen	Second Floor	30 m ²
Living Room/Kitchen	Second Floor	33 m ²
Living Room/Kitchen	Second Floor	28 m ²
Storage	Second Floor	1 m ²
Storage	Second Floor	1 m ²
Storage	Second Floor	1 m ²
Storage	Second Floor	1 m ²
Storage	Second Floor	1 m ²
Storage	Second Floor	7 m ²
Storage	Second Floor	1 m ²


Second Floor: 25

No.	Description	Date
CODE	SUITABILITY DESCRIPTION	
STATUS	PURPOSE OF ISSUE	
PROJECT		
IDD - Apartment Building		
TITLE		
Room Schedule - 2nd Floor		
CLIENT		
BCU Estates		
DRAWN BY G. M.	CHECKED BY G. M.	DATE Issue Date
SCALE (@A2) 1 : 100		PROJECT NUMBER INB202
DRAWING NUMBER A402		REV

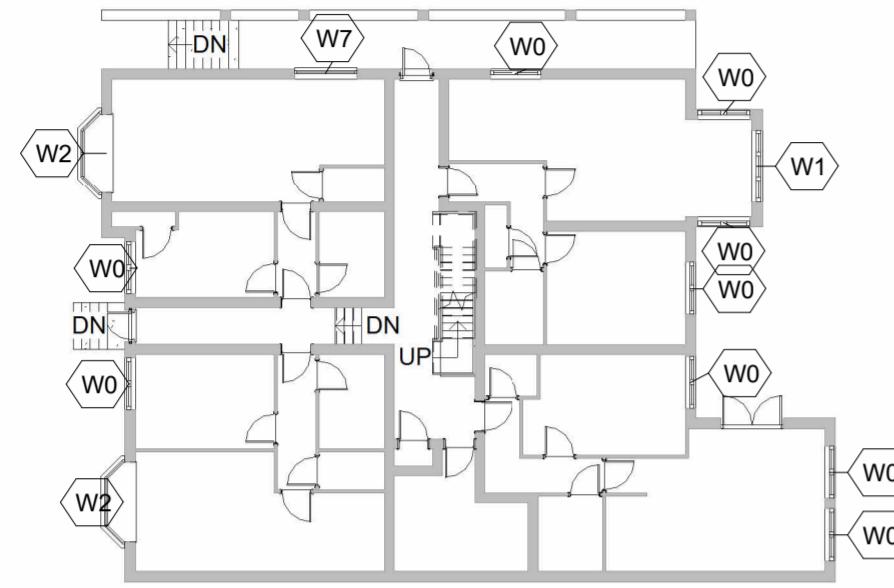


Ground Floor Window Tags

1 : 200

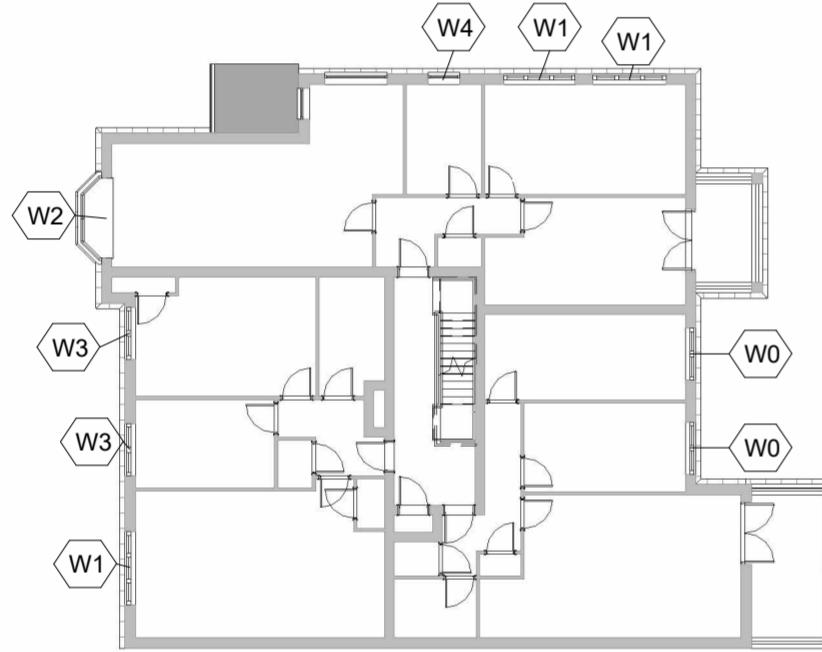

First Floor Window Tags

1 : 200

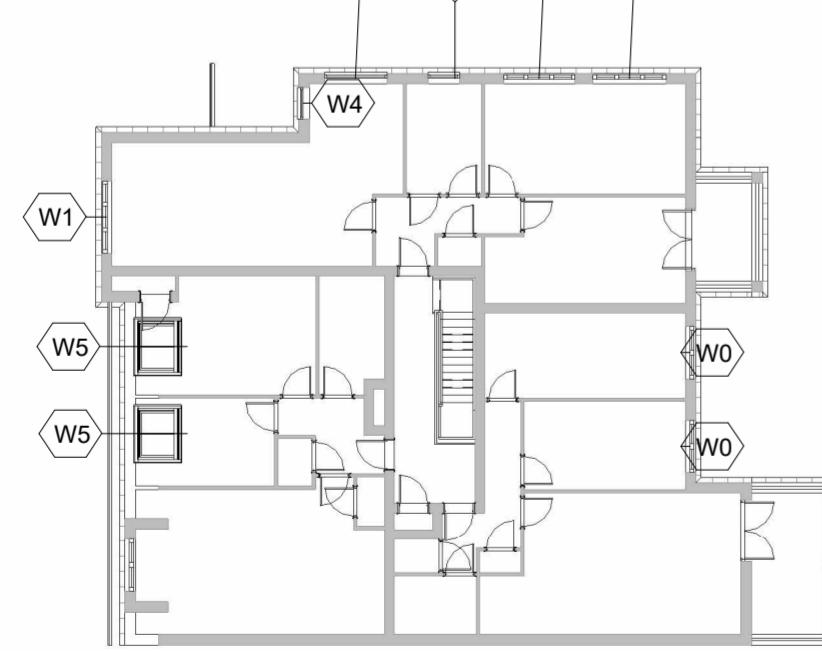

Second Floor Window Tags

1 : 200

Window Schedule		
Type Mark	Thermal Resistance (R)	Level

Lower ground

W0		Lower ground
W0		Lower ground
W2	0.2711 (m ² ·K)/W	Lower ground
W2	0.2711 (m ² ·K)/W	Lower ground
W7	0.1798 (m ² ·K)/W	Lower ground

Lower ground: 5

Ground Floor Window Tags

W0		Ground Floor Window Tags
W0		Ground Floor Window Tags
W0		Ground Floor Window Tags
W0		Ground Floor Window Tags
W0		Ground Floor Window Tags
W0		Ground Floor Window Tags
W0		Ground Floor Window Tags
W1		Ground Floor Window Tags

Ground Floor Window Tags: 8

First Floor

W0		First Floor
W0		First Floor
W1		First Floor
W1		First Floor
W1		First Floor
W2	0.2711 (m ² ·K)/W	First Floor
W3		First Floor
W3		First Floor
W4	0.1798 (m ² ·K)/W	First Floor
W4	0.1798 (m ² ·K)/W	First Floor
W7	0.1798 (m ² ·K)/W	First Floor

First Floor: 11

Window Schedule		
Type Mark	Thermal Resistance (R)	Level
WDF-100	0.8	A

Second Floor

W0		Second Floor
W0		Second Floor
W1		Second Floor
W1		Second Floor
W1		Second Floor
W3		Second Floor
W4	0.1798 ($m^2 \cdot K$)/W	Second Floor
W4	0.1798 ($m^2 \cdot K$)/W	Second Floor
W5	0.2711 ($m^2 \cdot K$)/W	Second Floor
W5	0.2711 ($m^2 \cdot K$)/W	Second Floor
W7	0.1798 ($m^2 \cdot K$)/W	Second Floor


Second Floor: 1

Roof Ridge

W6	$0.2711 \text{ (m}^2\cdot\text{K)}/\text{W}$	Roof Ridge
W6	$0.2711 \text{ (m}^2\cdot\text{K)}/\text{W}$	Roof Ridge


Roof Ridge: 2

<table border="1" style="width: 100%; border-collapse: collapse; font-size: small;"> <thead> <tr> <th style="width: 15%;">No.</th> <th style="width: 60%;">Description</th> <th style="width: 25%;">Date</th> </tr> </thead> <tbody> <tr><td></td><td></td><td></td></tr> </tbody> </table>			No.	Description	Date	
No.	Description	Date	
CODE	SUITABILITY DESCRIPTION	
STATUS	PURPOSE OF ISSUE	
PROJECT IDD - Apartment Building	
TITLE Window Schedule	
CLIENT BCU Estates	
DRAWN BY G. M.	CHECKED BY G. M.	DATE Issue Date	
SCALE (@A2) 1 : 200		PROJECT NUMBER INB202	
DRAWING NUMBER A403		REV	

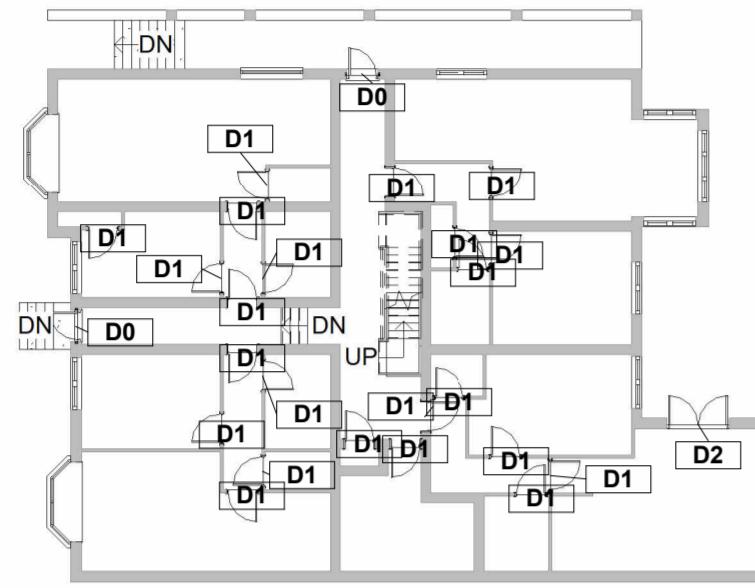


Ground Floor Door Tags

1 : 200

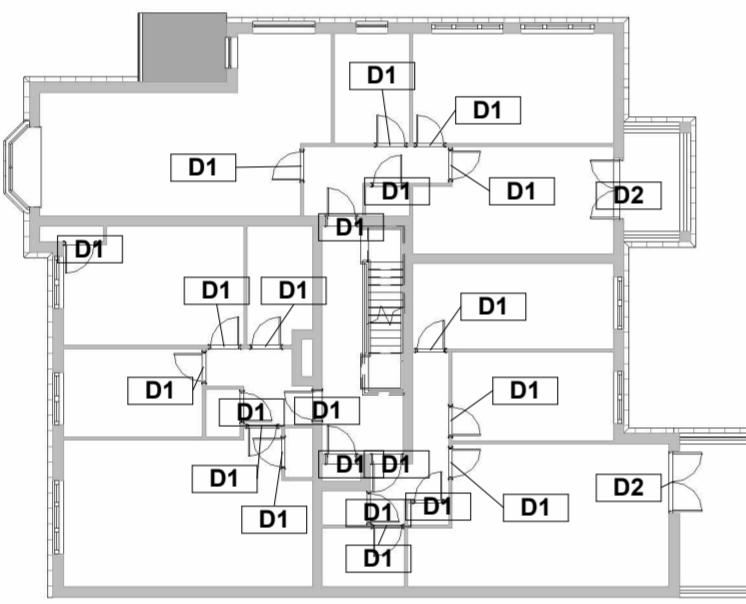

First Floor Door Tags

1 : 200

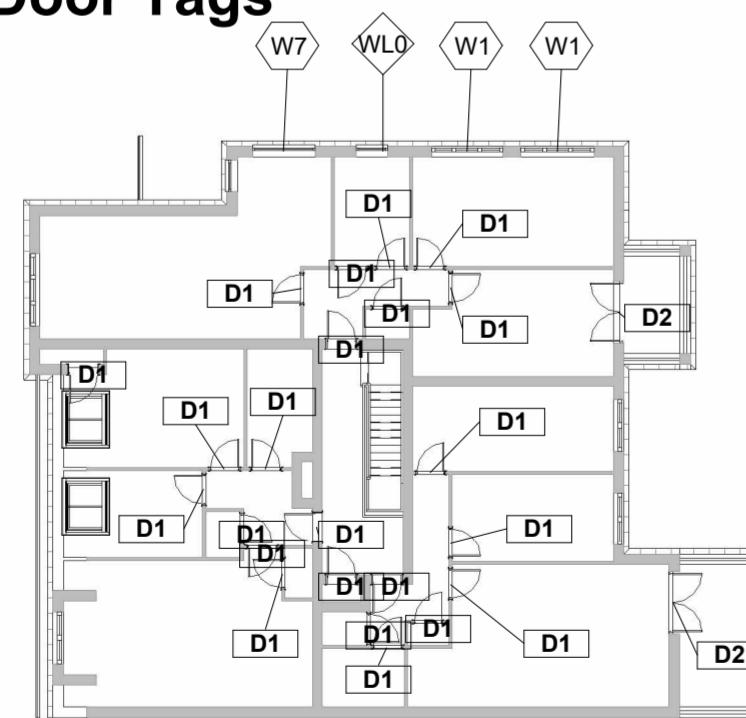

Second Floor Door Tags

1 : 200

Door Schedule		
Type Mark	Level	Thermal Resistance (R)

Lower ground

D0	Lower ground	0.1798 (m²·K)/W
D1	Lower ground	0.2701 (m²·K)/W
D1	Lower ground	0.2701 (m²·K)/W
D1	Lower ground	0.2701 (m²·K)/W
D1	Lower ground	0.2701 (m²·K)/W
D1	Lower ground	0.2701 (m²·K)/W
D1	Lower ground	0.2701 (m²·K)/W
D1	Lower ground	0.2701 (m²·K)/W
D1	Lower ground	0.2701 (m²·K)/W
D1	Lower ground	0.2701 (m²·K)/W
D1	Lower ground	0.2701 (m²·K)/W
D1	Lower ground	0.2701 (m²·K)/W
D1	Lower ground	0.2701 (m²·K)/W
D1	Lower ground	0.2701 (m²·K)/W
D1	Lower ground	0.2701 (m²·K)/W
D1	Lower ground	0.2701 (m²·K)/W

12

Ground Floor Window Tags

D0	Ground Floor Window Tags	0.1798 (m²·K)/W
D1	Ground Floor Window Tags	0.2701 (m²·K)/W
D1	Ground Floor Window Tags	0.2701 (m²·K)/W
D1	Ground Floor Window Tags	0.2701 (m²·K)/W
D1	Ground Floor Window Tags	0.2701 (m²·K)/W
D1	Ground Floor Window Tags	0.2701 (m²·K)/W
D1	Ground Floor Window Tags	0.2701 (m²·K)/W
D1	Ground Floor Window Tags	0.2701 (m²·K)/W
D1	Ground Floor Window Tags	0.2701 (m²·K)/W
D1	Ground Floor Window Tags	0.2701 (m²·K)/W
D1	Ground Floor Window Tags	0.2701 (m²·K)/W
D1	Ground Floor Window Tags	0.2701 (m²·K)/W
D1	Ground Floor Window Tags	0.2701 (m²·K)/W
D1	Ground Floor Window Tags	0.2701 (m²·K)/W
D1	Ground Floor Window Tags	0.2701 (m²·K)/W
D1	Ground Floor Window Tags	0.2701 (m²·K)/W
D1	Ground Floor Window Tags	0.2701 (m²·K)/W
D2	Ground Floor Window Tags	0.2711 (m²·K)/W
D2	Ground Floor Window Tags	0.2711 (m²·K)/W

Door Schedule		
Type Mark	Level	Thermal Resistance (R)

14

First Floor

D1	First Floor	0.2701 (m²·K)/W
D1	First Floor	0.2701 (m²·K)/W
D1	First Floor	0.2701 (m²·K)/W
D1	First Floor	0.2701 (m²·K)/W
D1	First Floor	0.2701 (m²·K)/W
D1	First Floor	0.2701 (m²·K)/W
D1	First Floor	0.2701 (m²·K)/W
D1	First Floor	0.2701 (m²·K)/W
D1	First Floor	0.2701 (m²·K)/W
D1	First Floor	0.2701 (m²·K)/W
D1	First Floor	0.2701 (m²·K)/W
D1	First Floor	0.2701 (m²·K)/W
D1	First Floor	0.2701 (m²·K)/W
D1	First Floor	0.2701 (m²·K)/W
D1	First Floor	0.2701 (m²·K)/W
D1	First Floor	0.2701 (m²·K)/W
D1	First Floor	0.2701 (m²·K)/W
D1	First Floor	0.2701 (m²·K)/W
D1	First Floor	0.2701 (m²·K)/W
D1	First Floor	0.2701 (m²·K)/W
D1	First Floor	0.2701 (m²·K)/W
D1	First Floor	0.2701 (m²·K)/W
D1	First Floor	0.2701 (m²·K)/W
D2	First Floor	0.2711 (m²·K)/W
D2	First Floor	0.2711 (m²·K)/W

24

Second Floor

D1	Second Floor	0.2701 (m²·K)/W
D1	Second Floor	0.2701 (m²·K)/W
D1	Second Floor	0.2701 (m²·K)/W
D1	Second Floor	0.2701 (m²·K)/W
D1	Second Floor	0.2701 (m²·K)/W
D1	Second Floor	0.2701 (m²·K)/W
D1	Second Floor	0.2701 (m²·K)/W
D1	Second Floor	0.2701 (m²·K)/W
D1	Second Floor	0.2701 (m²·K)/W
D1	Second Floor	0.2701 (m²·K)/W
D1	Second Floor	0.2701 (m²·K)/W
D1	Second Floor	0.2701 (m²·K)/W
D1	Second Floor	0.2701 (m²·K)/W
D1	Second Floor	0.2701 (m²·K)/W
D1	Second Floor	0.2701 (m²·K)/W
D1	Second Floor	0.2701 (m²·K)/W
D1	Second Floor	0.2701 (m²·K)/W
D1	Second Floor	0.2701 (m²·K)/W
D1	Second Floor	0.2701 (m²·K)/W
D1	Second Floor	0.2701 (m²·K)/W
D1	Second Floor	0.2701 (m²·K)/W
D1	Second Floor	0.2701 (m²·K)/W
D1	Second Floor	0.2701 (m²·K)/W
D1	Second Floor	0.2701 (m²·K)/W
D1	Second Floor	0.2701 (m²·K)/W
D1	Second Floor	0.2701 (m²·K)/W
D1	Second Floor	0.2701 (m²·K)/W
D1	Second Floor	0.2701 (m²·K)/W
D1	Second Floor	0.2701 (m²·K)/W
D2	Second Floor	0.2711 (m²·K)/W
D2	Second Floor	0.2711 (m²·K)/W

25

75

--	--	--

No.	Description	Date
-----	-------------	------

CODE	SUITABILITY DESCRIPTION
STATUS	PURPOSE OF ISSUE

PROJECT
IDD - Apartment Building


TITLE
Door Schedule

CLIENT
BCU Estates

DRAWN BY G. M.	CHECKED BY G. M.	DATE Issue Date
-------------------	---------------------	--------------------


SCALE (@A2) 1 : 200	PROJECT NUMBER INB202
------------------------	--------------------------

DRAWING NUMBER A404	REV
------------------------	-----

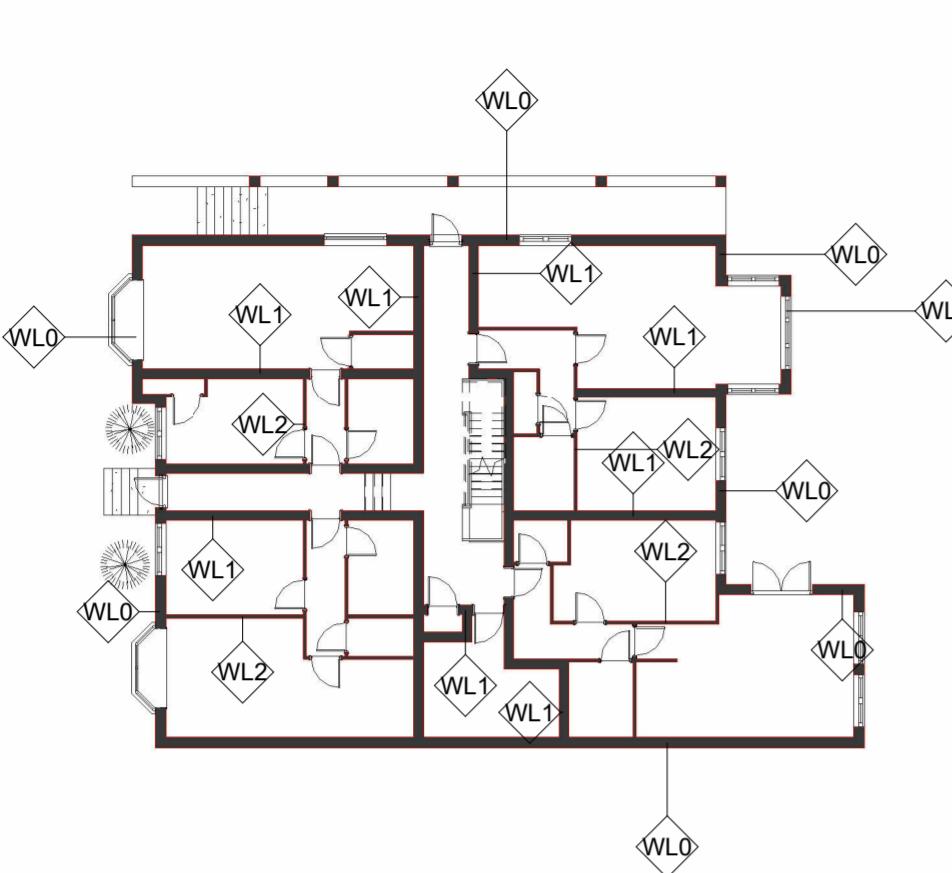


Ground Floor Wall Tags

1 : 200

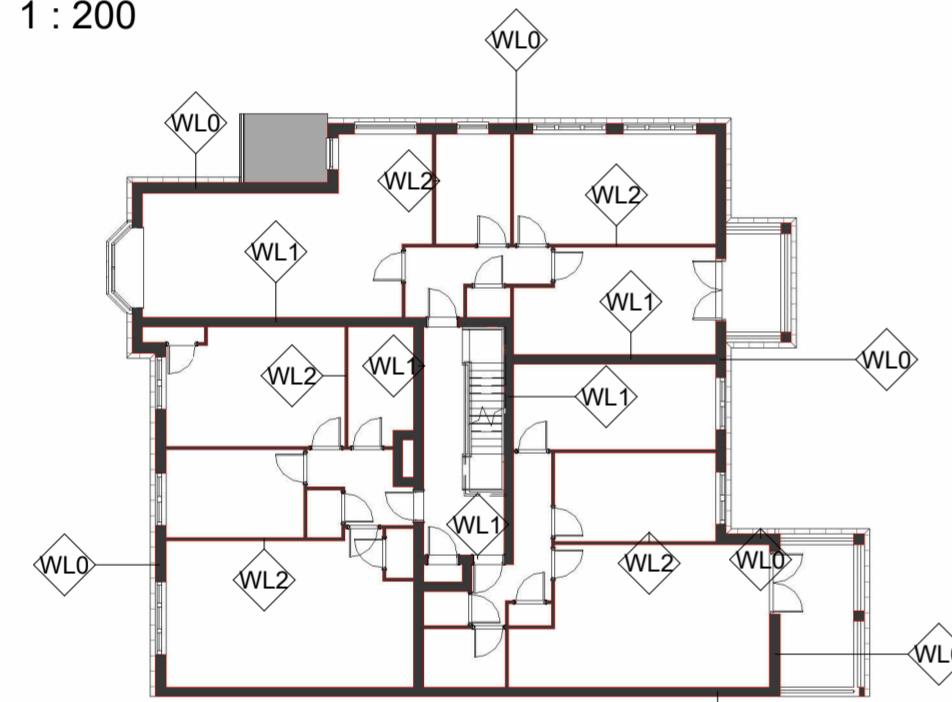

First Floor Wall Tag

1 : 200

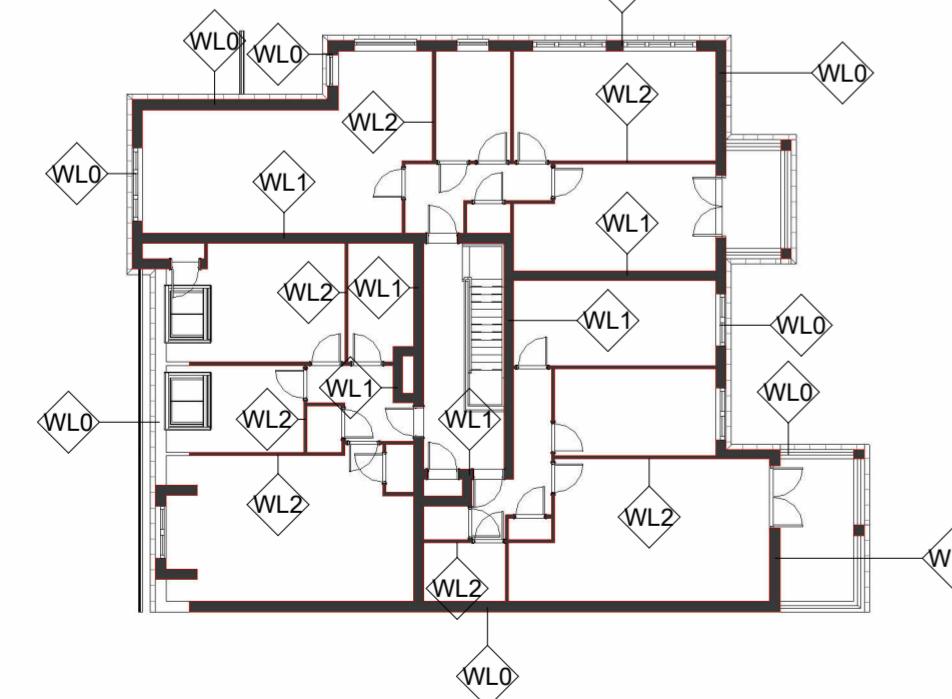

Second Floor Wall Tags

1 : 200

Wall Schedule

WL0	Lower ground
WL1	Lower ground
WL1	Lower ground

Wall Schedule

WL1	Lower ground
WL2	Lower ground
WL3	Lower ground
WL3	Lower ground
WL3	Lower ground

Wall Schedule

Wall Schedule

WL2	First Floor
WL3	First Floor

A large, empty rectangular frame occupies most of the page, defined by a thin black border. The interior of the frame is completely white and devoid of any text, figures, or tables.


CODE	SUITABILITY DESCRIPTION
STATUS	PURPOSE OF ISSUE

PROJECT

TITLE


CLIENT BCU Estates

DRAWN BY G. M.	CHECKED BY G. M.	DATE Issue Date
SCALE (@A2) 1 : 200		PROJECT NUMBER INB202
DRAWING NUMBER A405		REV

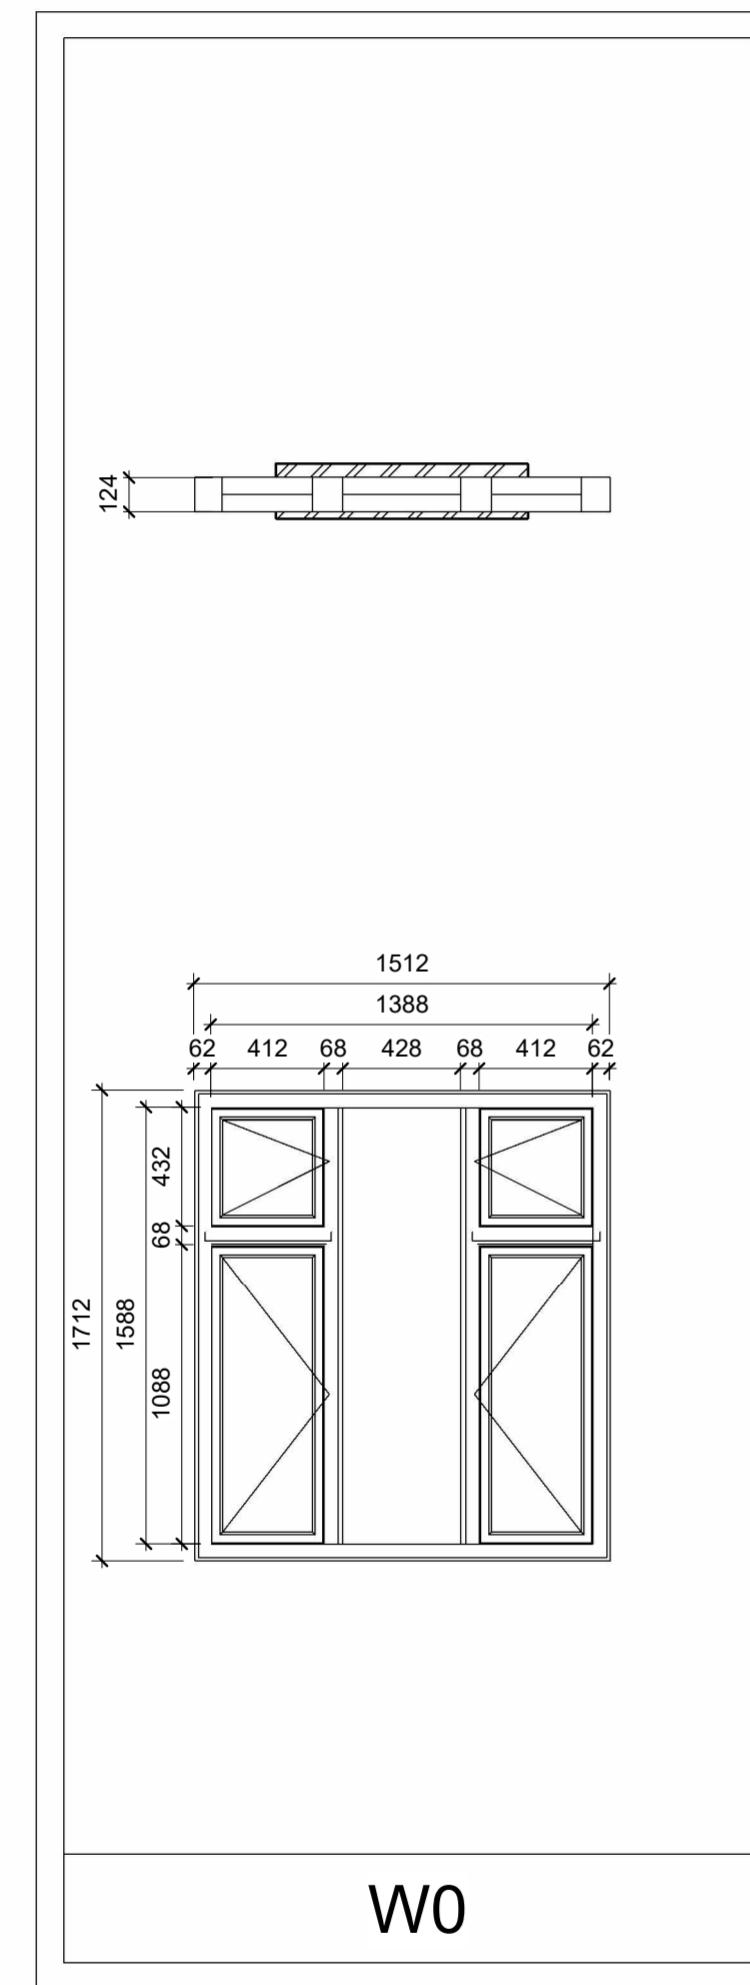


Window Element Key

1 : 25

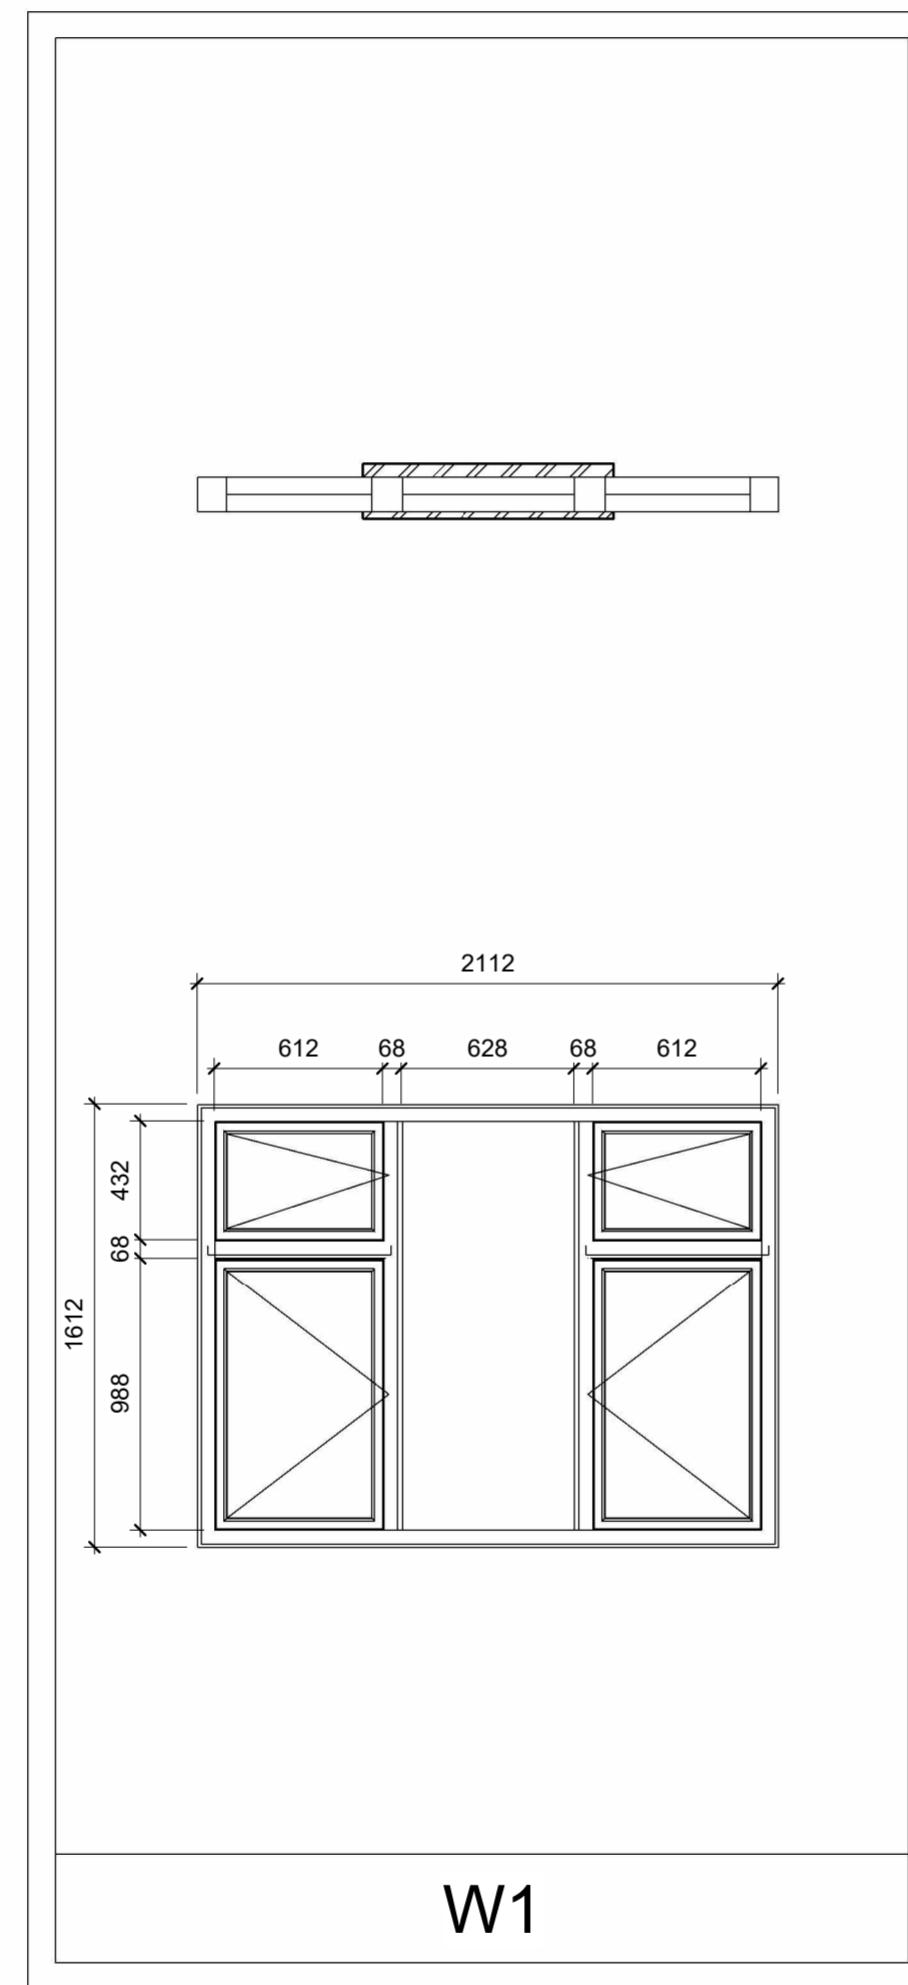


W1

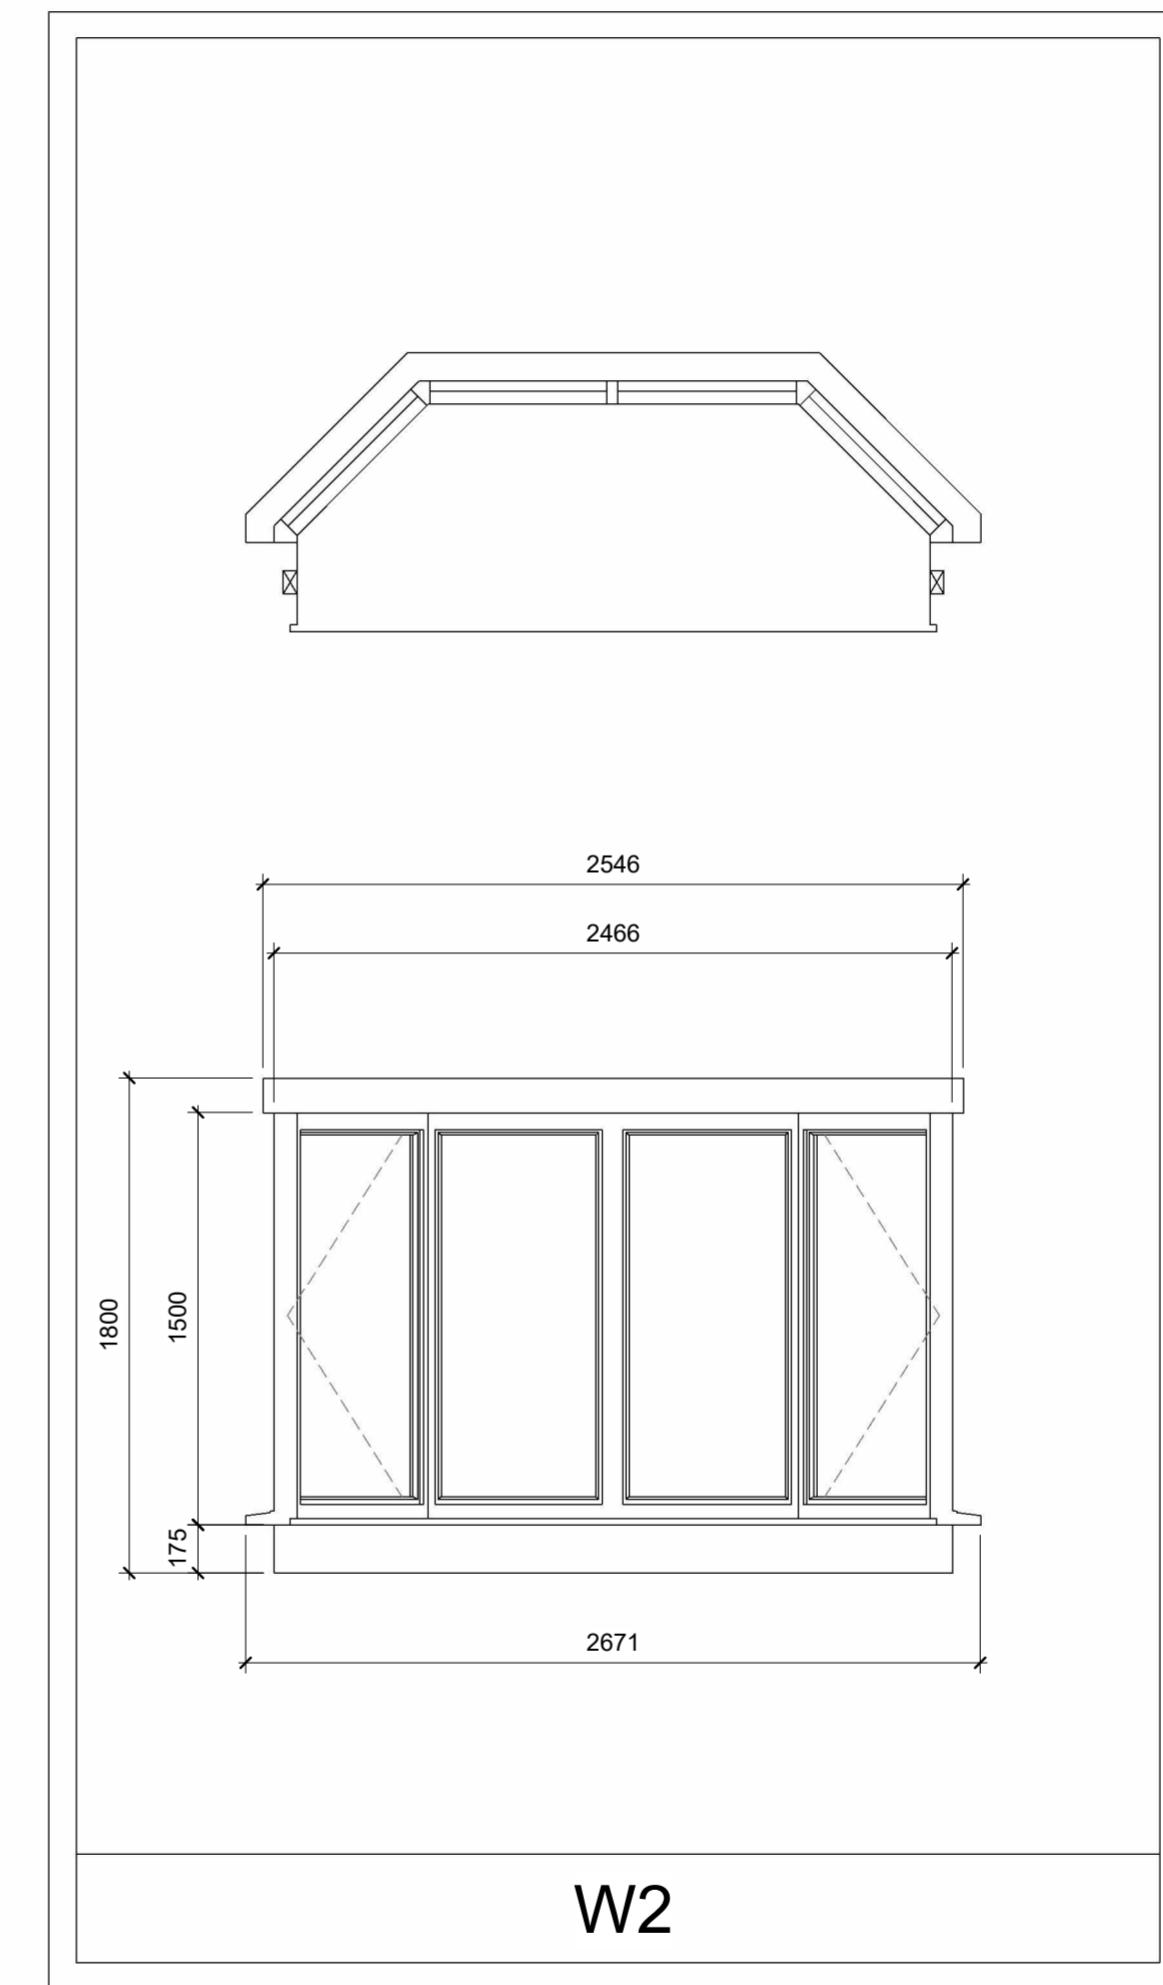

W2


No.	Description
CODE	SUITABILITY DESCRIPTION
STATUS	PURPOSE OF ISSUE
PROJECT	
IDD - Apartment Building	
TITLE	
Element Key - Windows	
CLIENT	
BCU Estates	
DRAWN BY G. M.	CHECKED BY G. M.
SCALE (@A2) 1 : 25	DATE Issue Date PROJECT NUMBER INB202
DRAWING NUMBER A500	REV

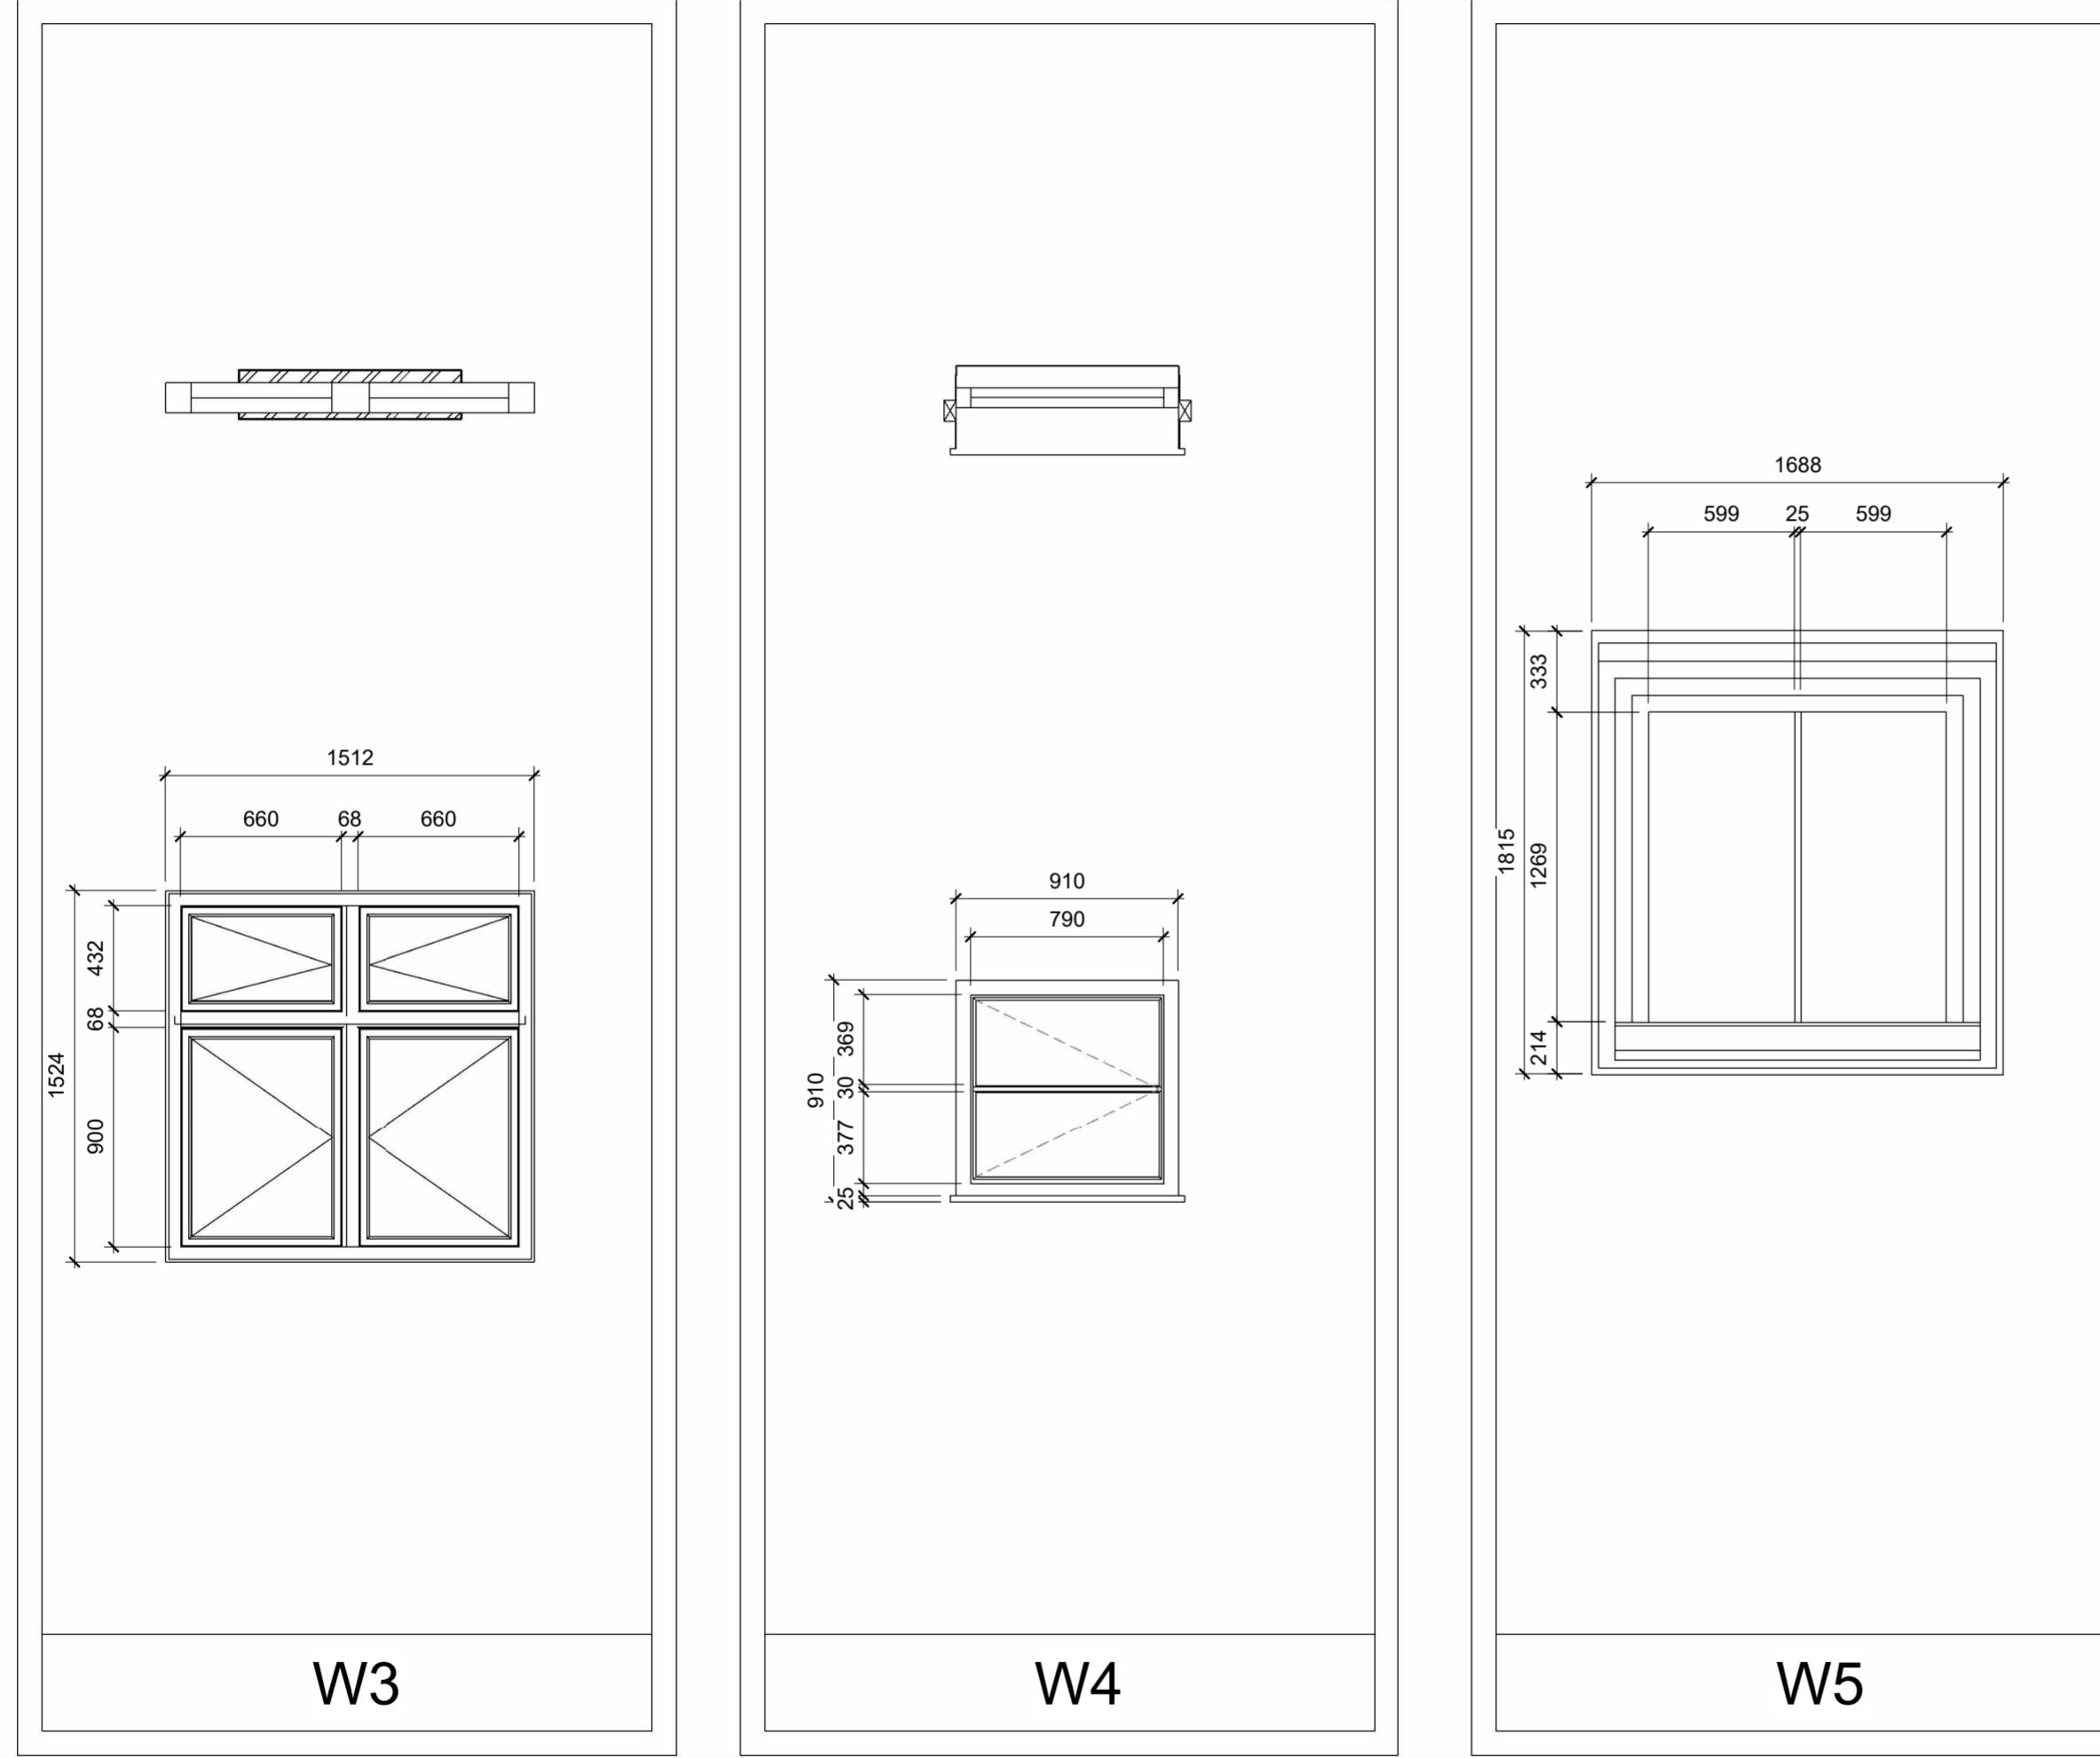

Window Element Key 2


1 : 25

No.	Description	Date
CODE	SUITABILITY DESCRIPTION	
STATUS	PURPOSE OF ISSUE	
PROJECT		
IDD - Apartment Building		
TITLE		
Element Key - Windows 2		
CLIENT		
BCU Estates		
DRAWN BY G. M.	CHECKED BY G. M.	DATE Issue Date
SCALE (@A2) 1 : 25		PROJECT NUMBER INB202
DRAWING NUMBER A501		REV

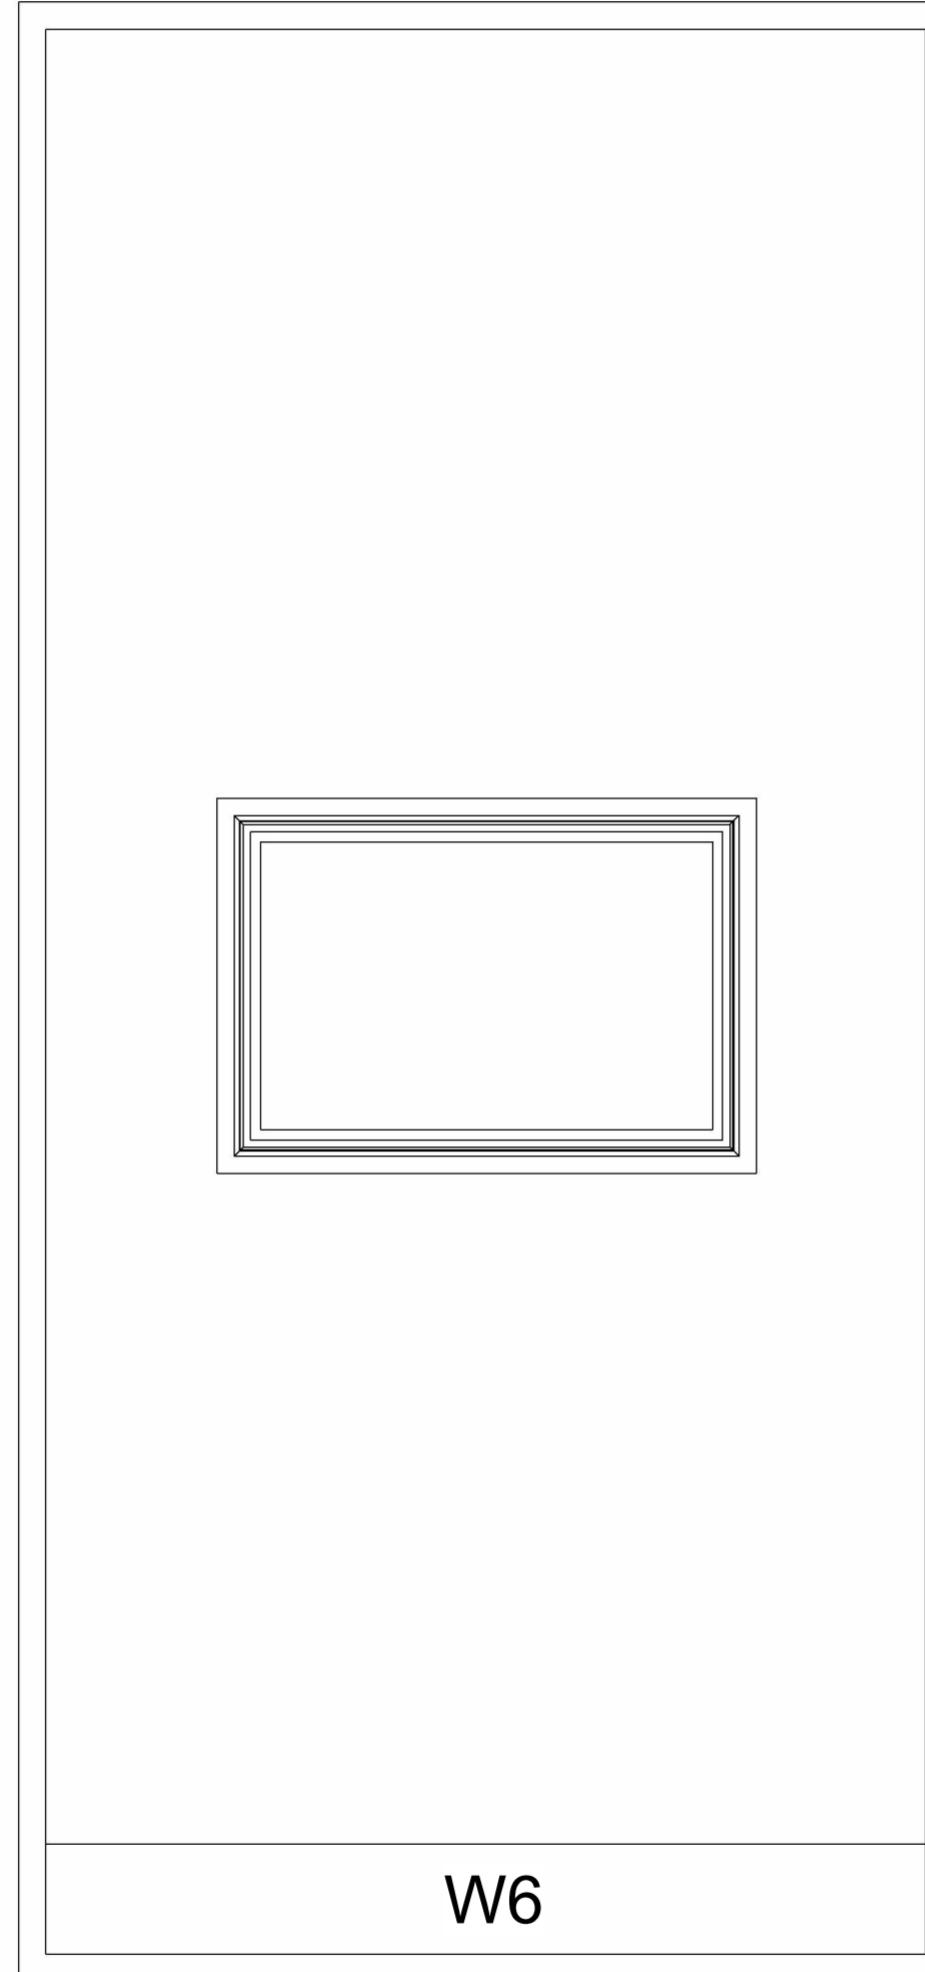


Window Element Key 3


1 : 25

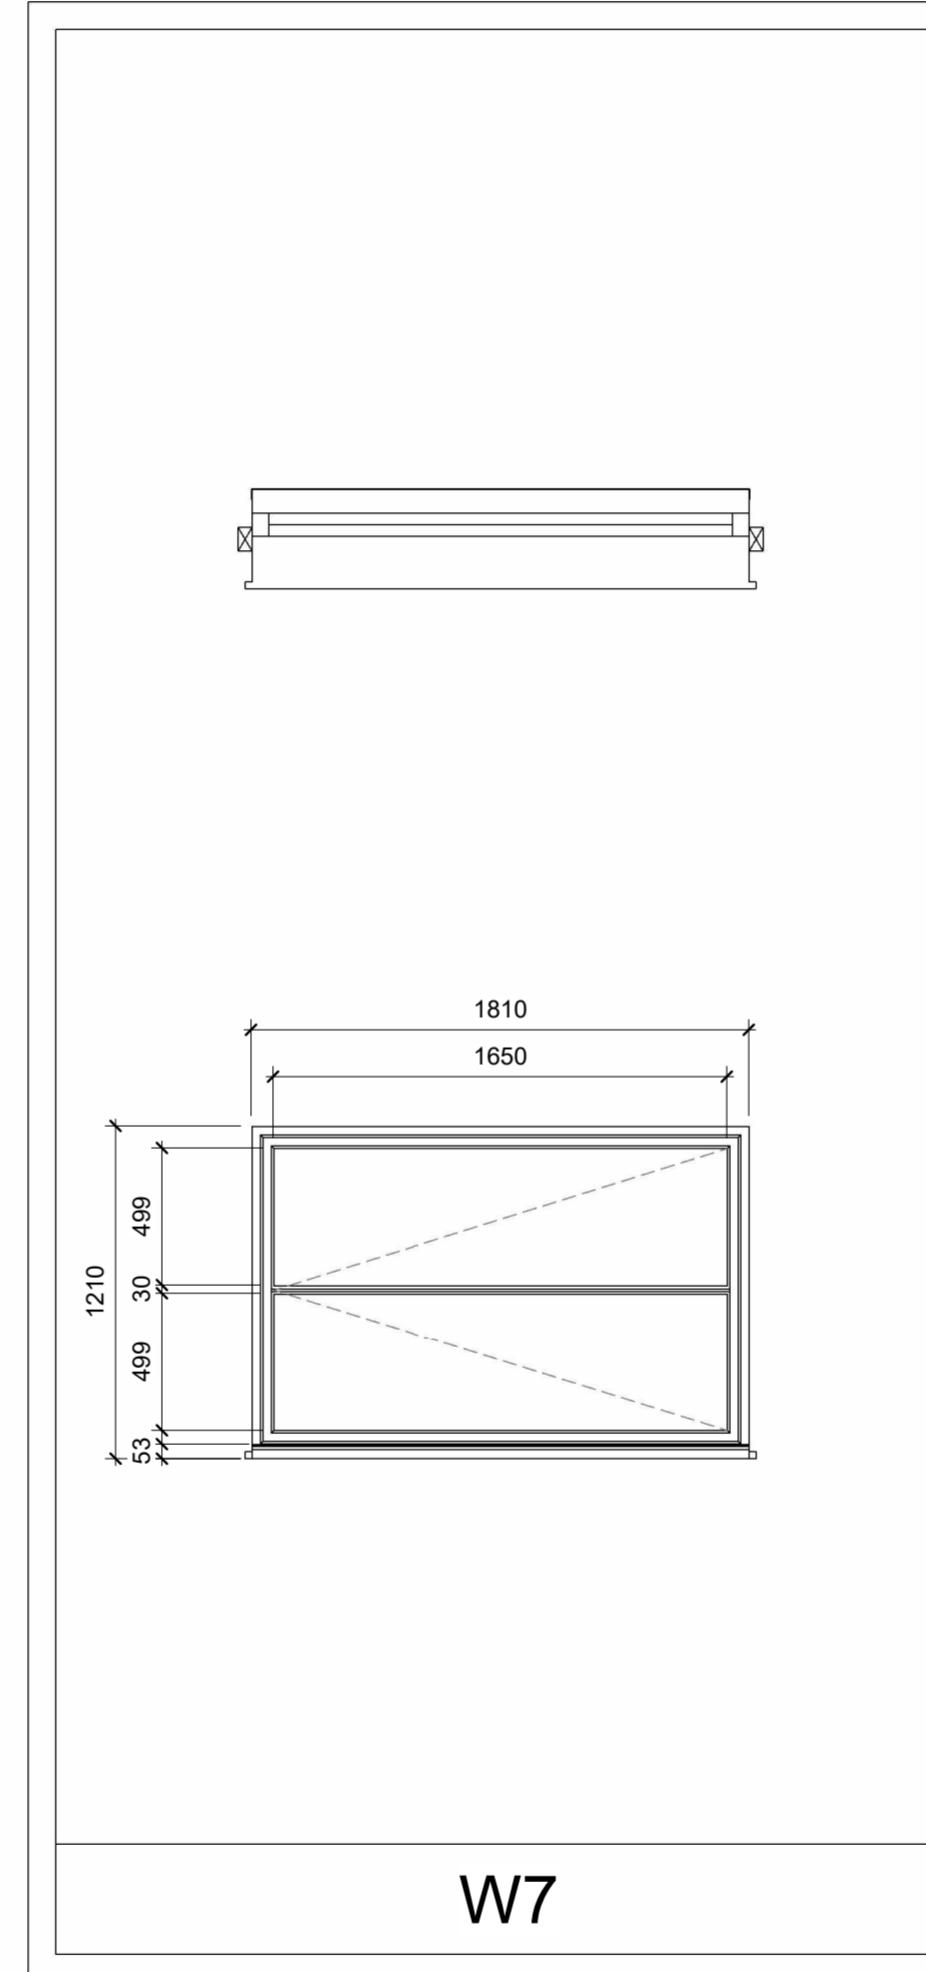


No.	Description
CODE	SUITABILITY DESCRIPTION
STATUS	PURPOSE OF ISSUE
PROJECT	
IDD - Apartment Building	
TITLE	
Element Key - Windows 3	
CLIENT	
BCU Estates	
DRAWN BY G. M.	CHECKED BY G. M.
SCALE (@A2) 1 : 25	DATE Issue Date PROJECT NUMBER INB202
DRAWING NUMBER A502	REV

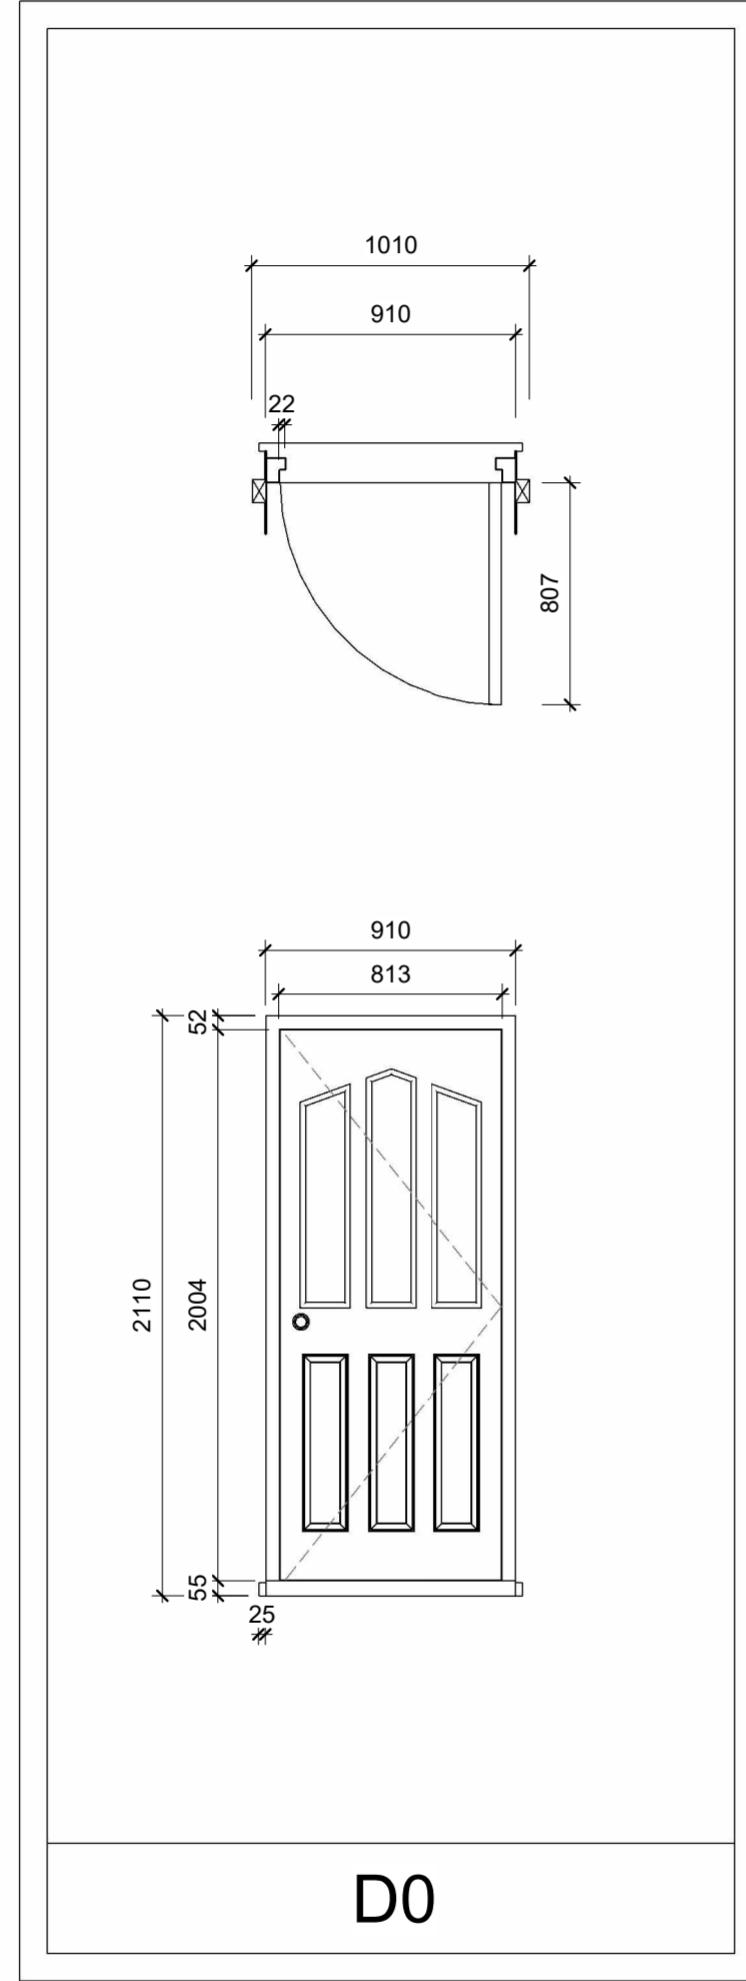

Door Element Key

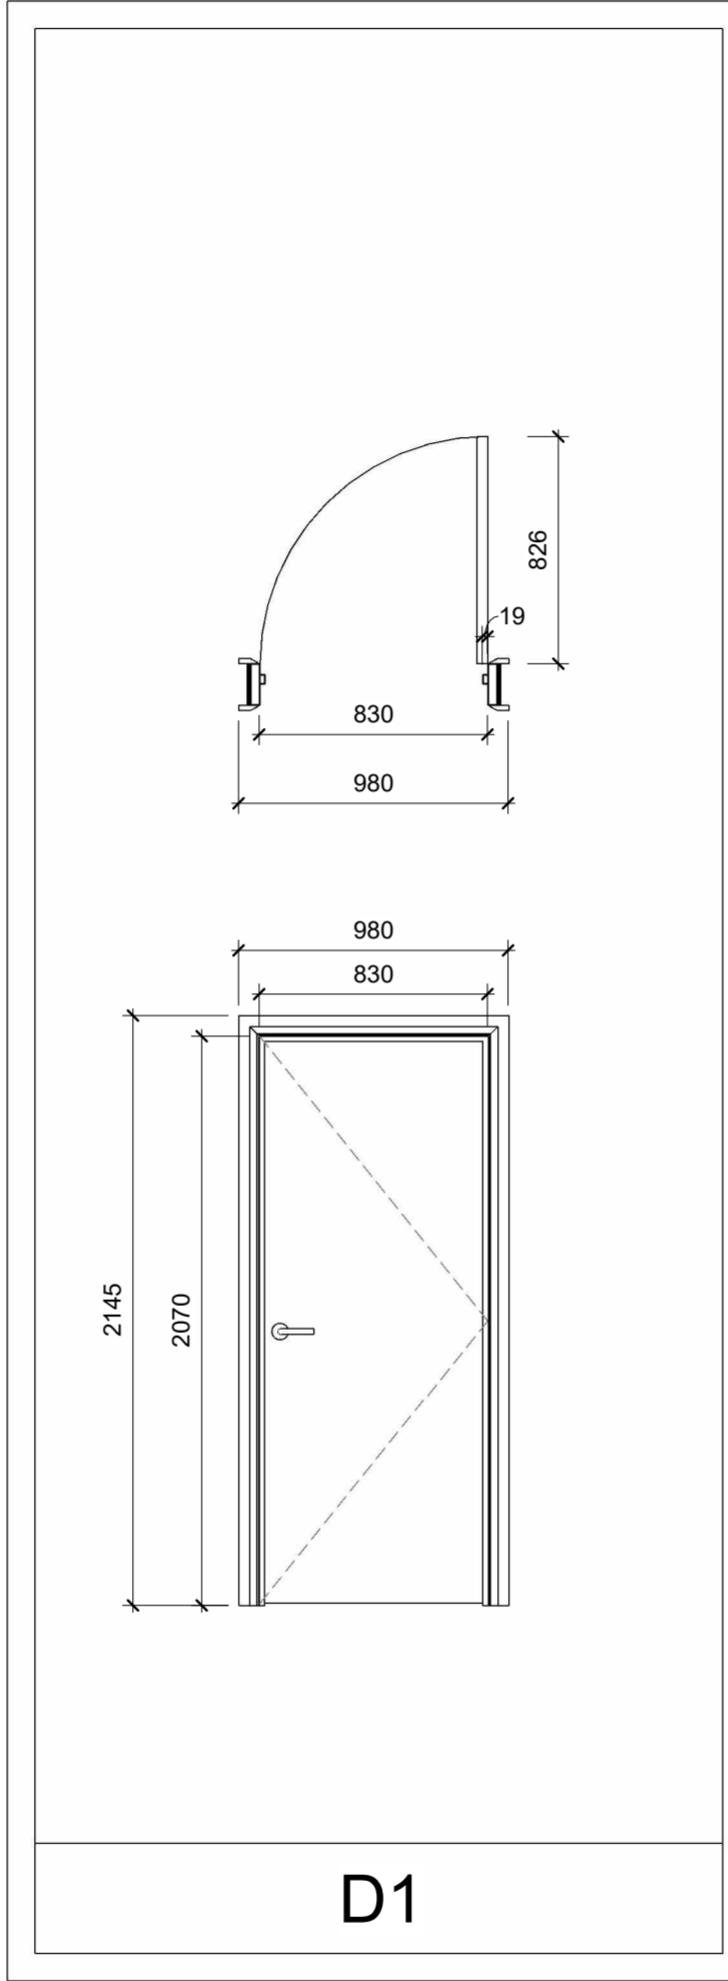

D1

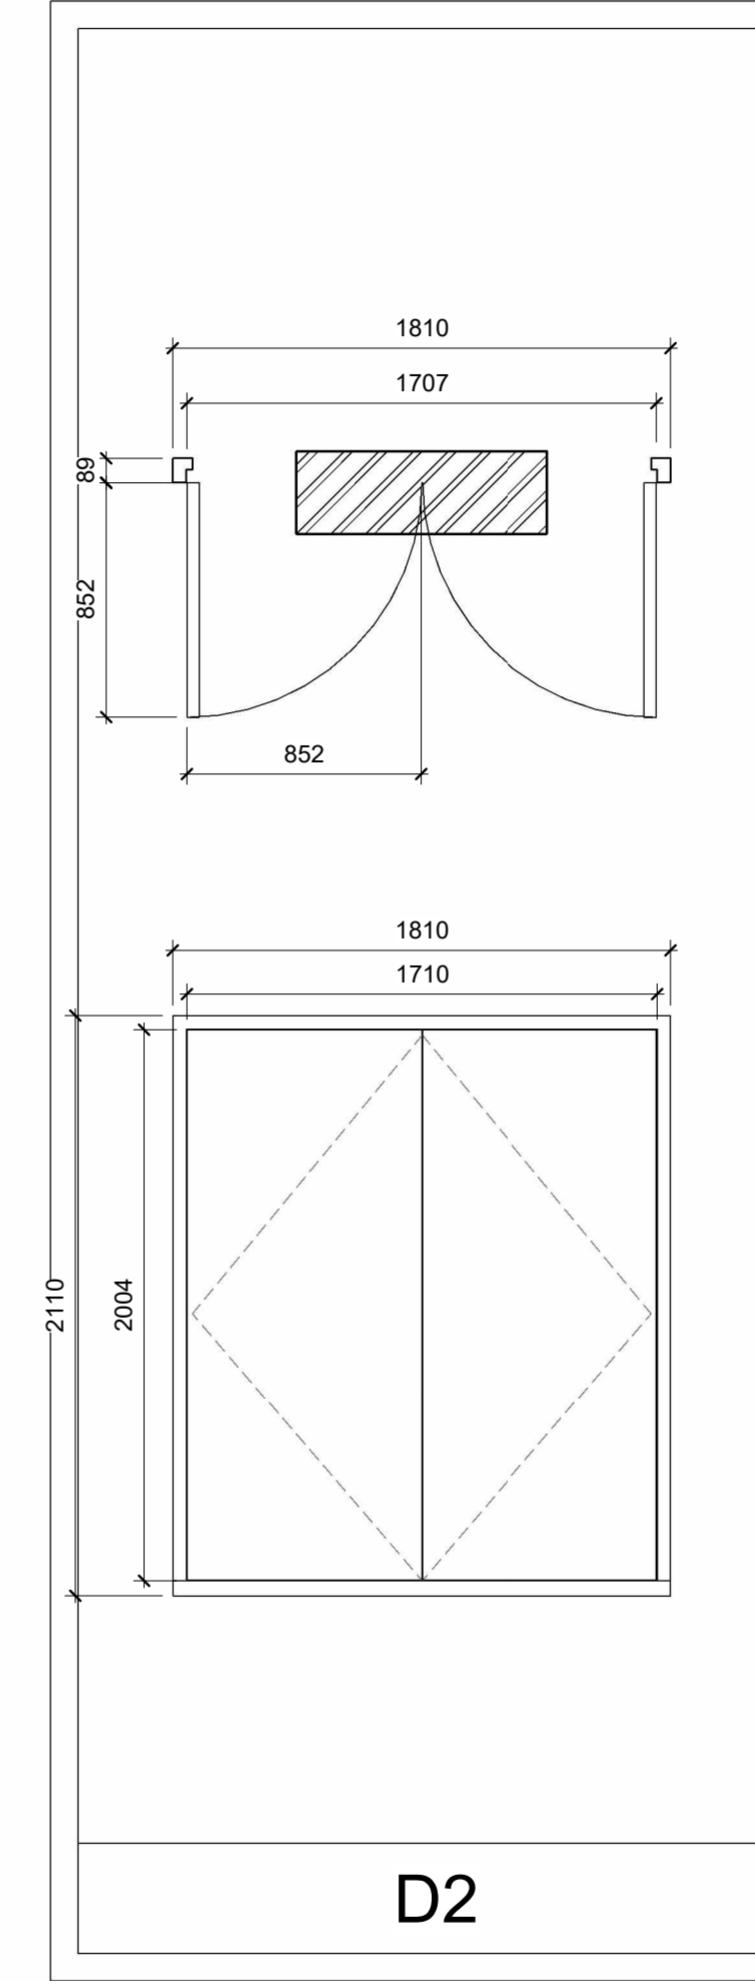

D2

11/05/2023 13:56:50



CODE	SUITABILITY DESCRIPTION
------	-------------------------

IDD - Apartment Building


TITLE

3D Render 1

CLIENT

BCU Estates

DRAWN BY G. M.	CHECKED BY G. M.	DATE Issue Date
SCALE (@A2)		PROJECT NUMBER INB202
DRAWING NUMBER A600		REV

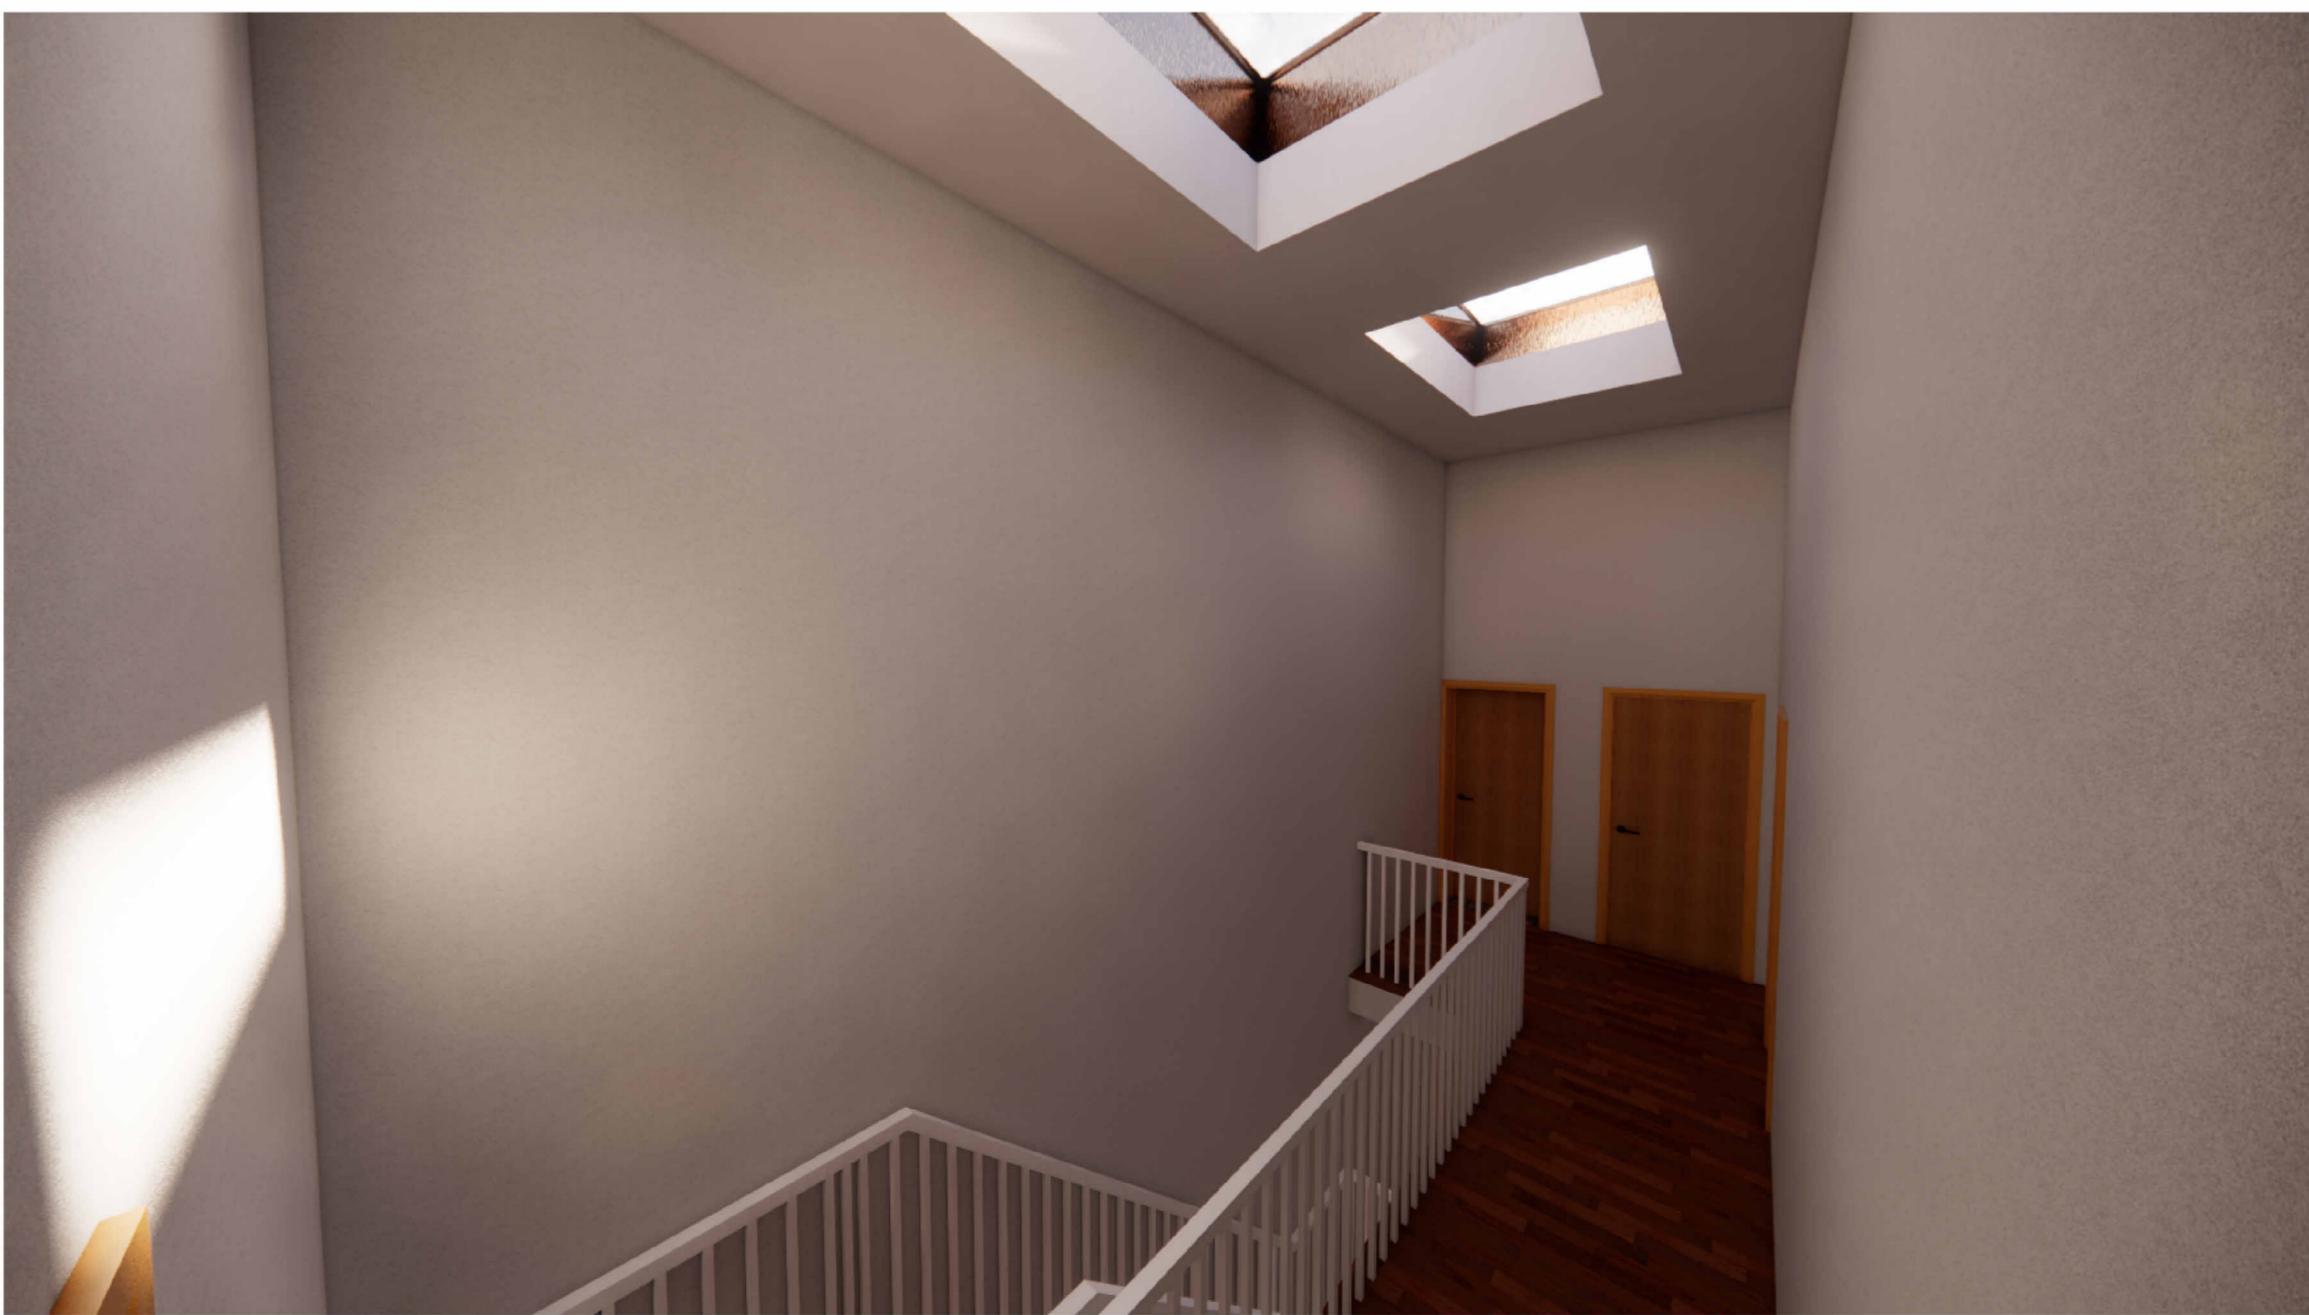

CODE	SUITABILITY DESCRIPTION
------	-------------------------

STATUS	PURPOSE OF ISSUE
--------	------------------

For more information about the study, please contact the study team at 1-800-258-4929 or visit www.cancer.gov.

PROJECT

IDD - Apartment Building

TITLE

3D Render 2

CLIENT

BCU Estates

DRAWN BY G. M.	CHECKED BY G. M.	DATE Issue Date
SCALE (@A2)		PROJECT NUMBER INB202
DRAWING NUMBER A601		REV



CODE	SUITABILITY DESCRIPTION
------	-------------------------

STATUS	PURPOSE OF ISSUE
--------	------------------

For more information about the study, please contact the study team at 1-800-258-4929 or visit www.cancer.gov.

PROJECT

IDD - Apartment Building



TITLE

3D Render 3

CLIENT

BCU Estates

DRAWN BY G. M.	CHECKED BY G. M.	DATE Issue Date
SCALE (@A2)		PROJECT NUMBER INB202
DRAWING NUMBER A602		REV

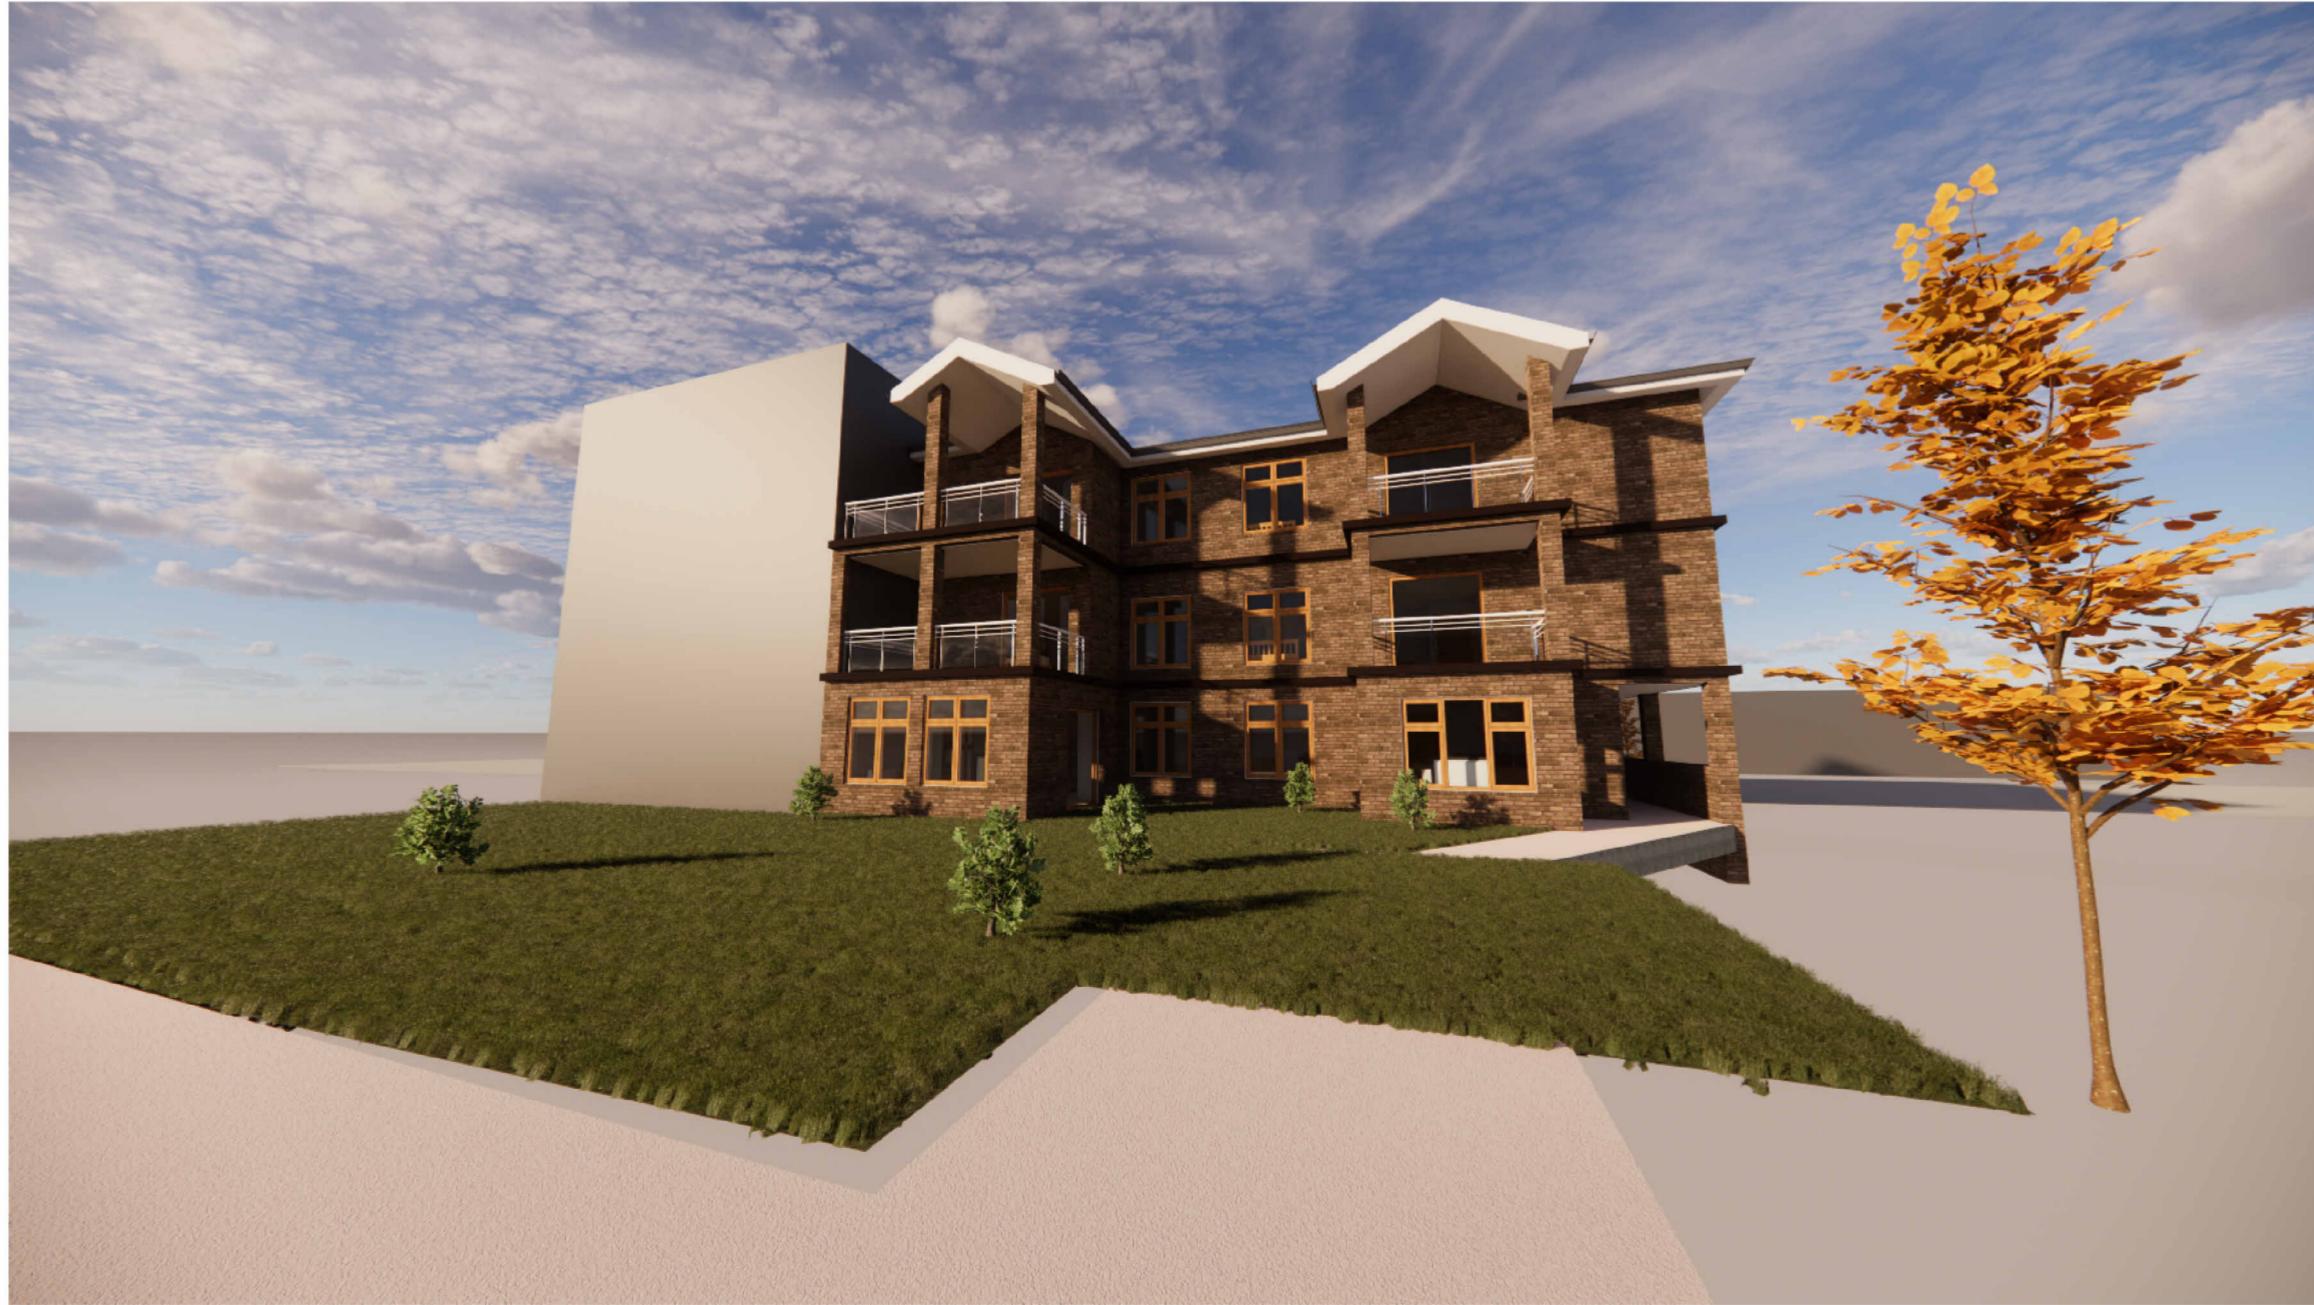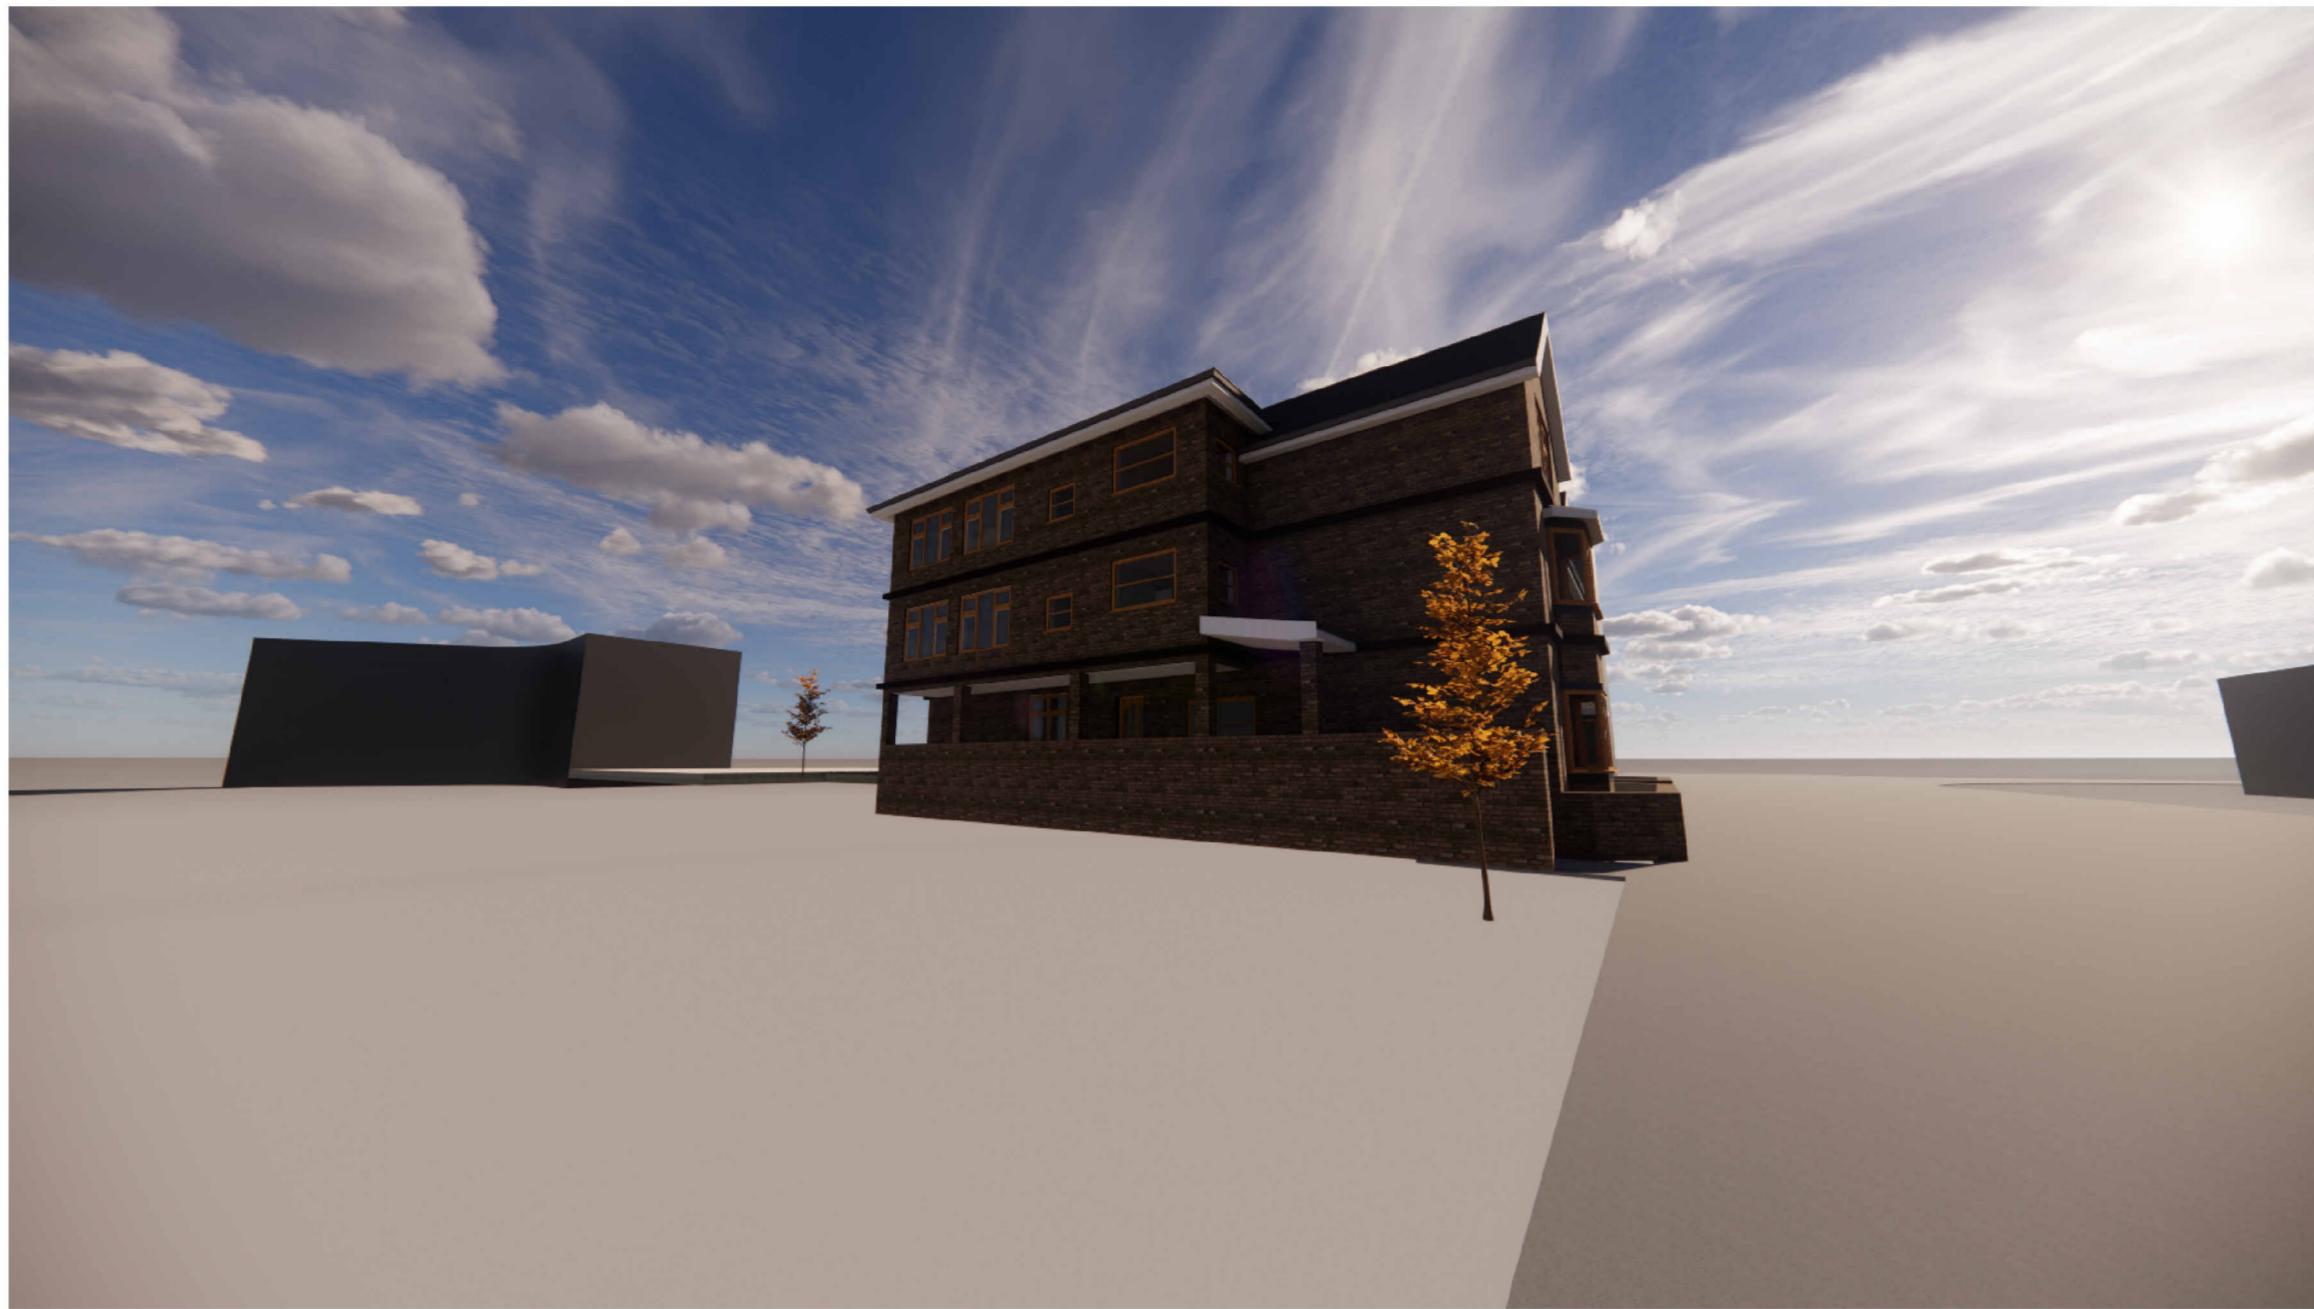

No.	Description	Date
CODE	SUITABILITY DESCRIPTION	
STATUS	PURPOSE OF ISSUE	
PROJECT		
IDD - Apartment Building		
TITLE		
3D Render 4		
CLIENT		
BCU Estates		
DRAWN BY G. M.	CHECKED BY G. M.	DATE Issue Date
SCALE (@A2)		PROJECT NUMBER INB202
DRAWING NUMBER A603		REV